

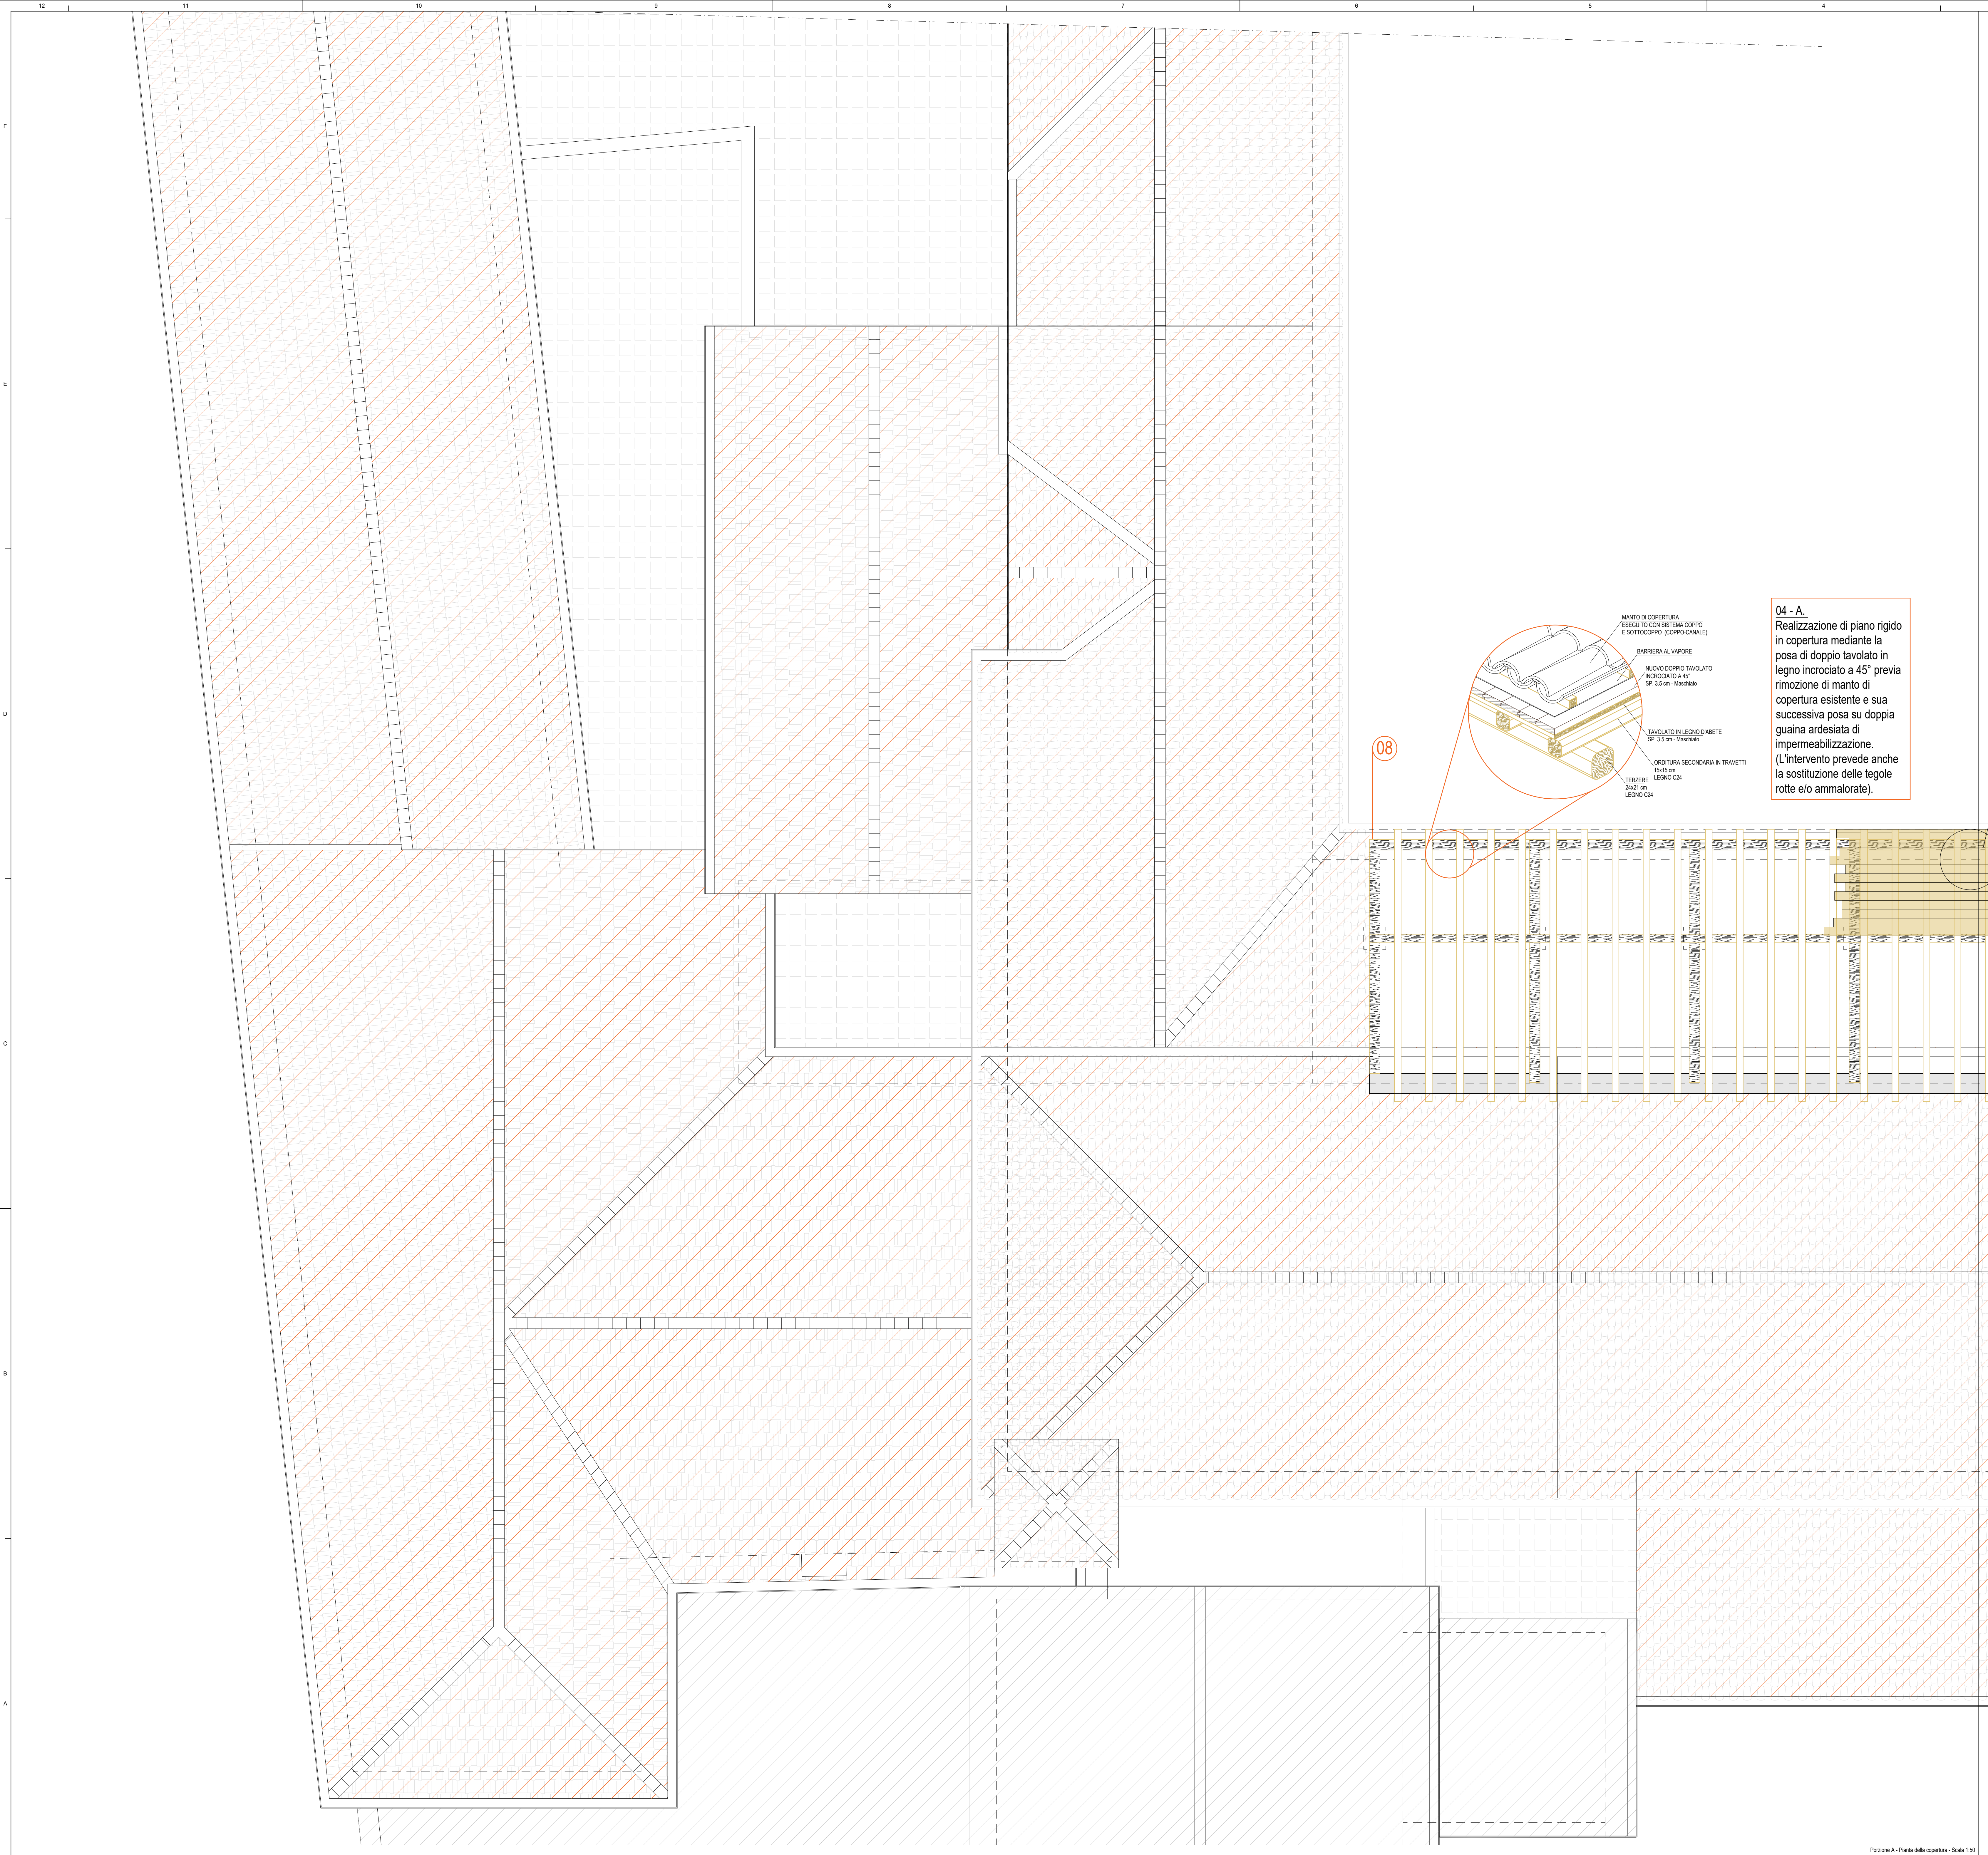


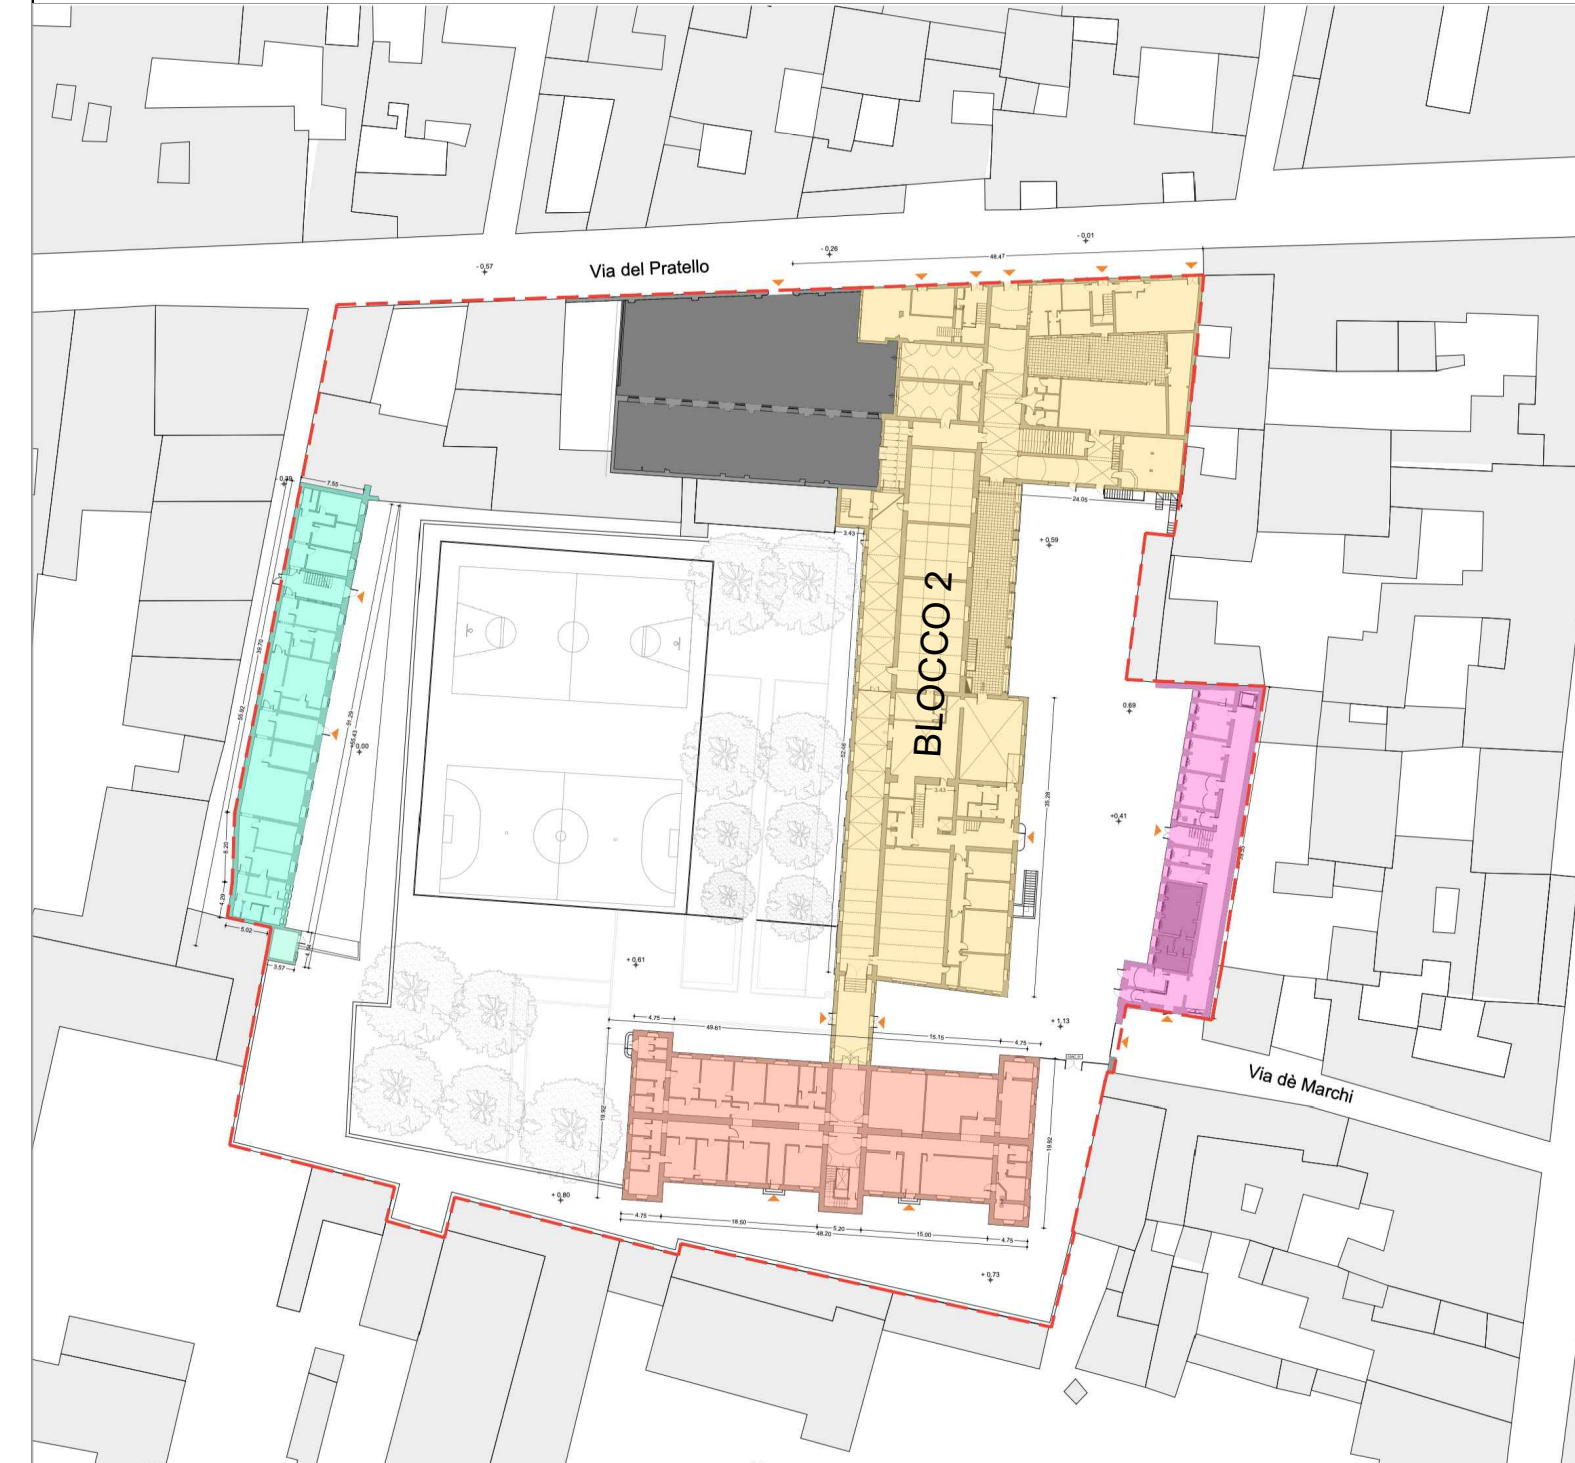

TIPOLOGIA DI INTERVENTO	LEGENDA DEGLI INTERVENTI	LEGENDA DEI RETINI	
		MURATURA PORTANTE	TRAVEZZI ESISTENTI
01. FASCE IN FIBRA DI ACCIAIO (INTONACO ARMATO)			
02. INTERVENTO SU MURATURE A SACCO (INTONACO ARMATO)			
03. FASCE IN FIBRA DI ACCIAIO APPLICATE SU UN SINGOLO LATO (INTONACO ARMATO)			
04. CERCANTURE DEI PILASTRI			
05. GIUNTO BERNINI			
06. CATENE IN ACCIAIO			
07. FASCE DI PIANO E IPO-ARMALI (o simili)			
08. PIANO RIGIDO IN COPERTURA			

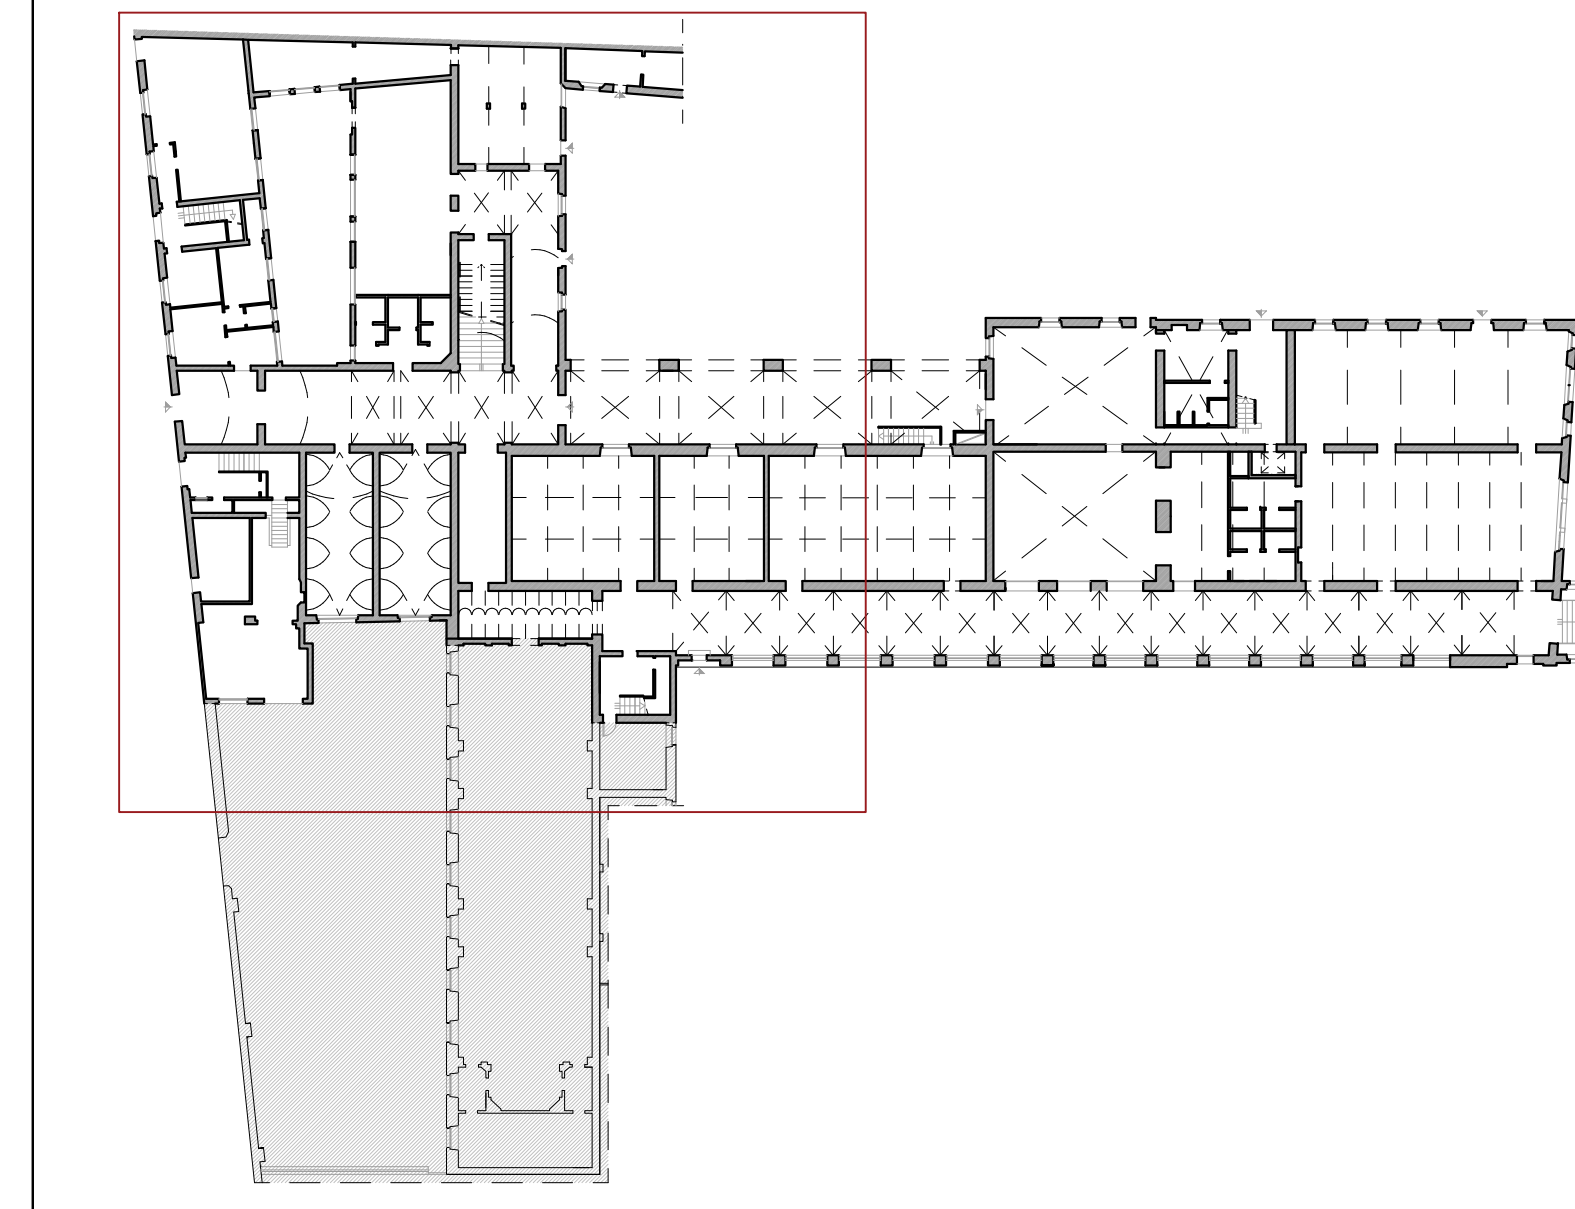

Finanziato dall'Unione europea
NextGenerationEU

Ministero delle infrastrutture e dei trasporti

Ministero delle Infrastrutture e dei Trasporti

Provveditorato Interregionale per le Opere Pubbliche Lombardia e Emilia Romagna
sede coordinata di Bologna - Piazza VIII Agosto, 26 - 40126 BOLOGNA974- PNC - BO 7322 - Affidamento della progettazione esecutiva ed esecuzione lavori per gli interventi di miglioramento sismico, efficientamento energetico ed adeguamento funzionale del carcere minorile in Via del Pratello a Bologna.
CUP D39J21022100006 CIG B2373792CA**IL RESPONSABILE UNICO DEL PROCEDIMENTO**
Dott. Ing. Roberto GAMBARDIA**IL DIRETTORE DELL'ESECUZIONE DEL CONTRATTO**
Dott. Ing. Roberto GAMBARDIA**Progettista incarico**
Progettista responsabile dell'integrazione tra le varie prestazioni specialistiche: [Arch. Paolo Meschini](#)
Progettista responsabile progetto architettonico: [Arch. Valterina Meschini](#)
Progettista responsabile progetto strutturale: [Arch. Silvio Meschini](#)
Progettista responsabile progetto impiantistico: [Arch. Paolo Meschini](#)
Consulente impianti: P.I. Eligo Dati**Studio AARC.it**
Via Giuseppe Mazzini 32
51122 Livorno (LI)**SICEA**
Via Benvenuto, 8
33010 Vigonza (PD)**CONTRAENTE**
SICEA
Via Benvenuto, 8
33010 Vigonza (PD)**Disciplina di progetto:**
ELABORATI STRUTTURALI
PROGETTO ESECUTIVO
PROGETTO - Blocco 2 - Planta Copertura Zona A e dettagli costruttivi
PE 2S.2.PC-PWT.221.00**SCALA** 1:50
DATA 02/12/2024**Nome file:**
Questo elaborato è di proprietà del Ministero delle Infrastrutture e delle Mobilità sostenibili non può essere riprodotto, anche parzialmente, senza autorizzazione