

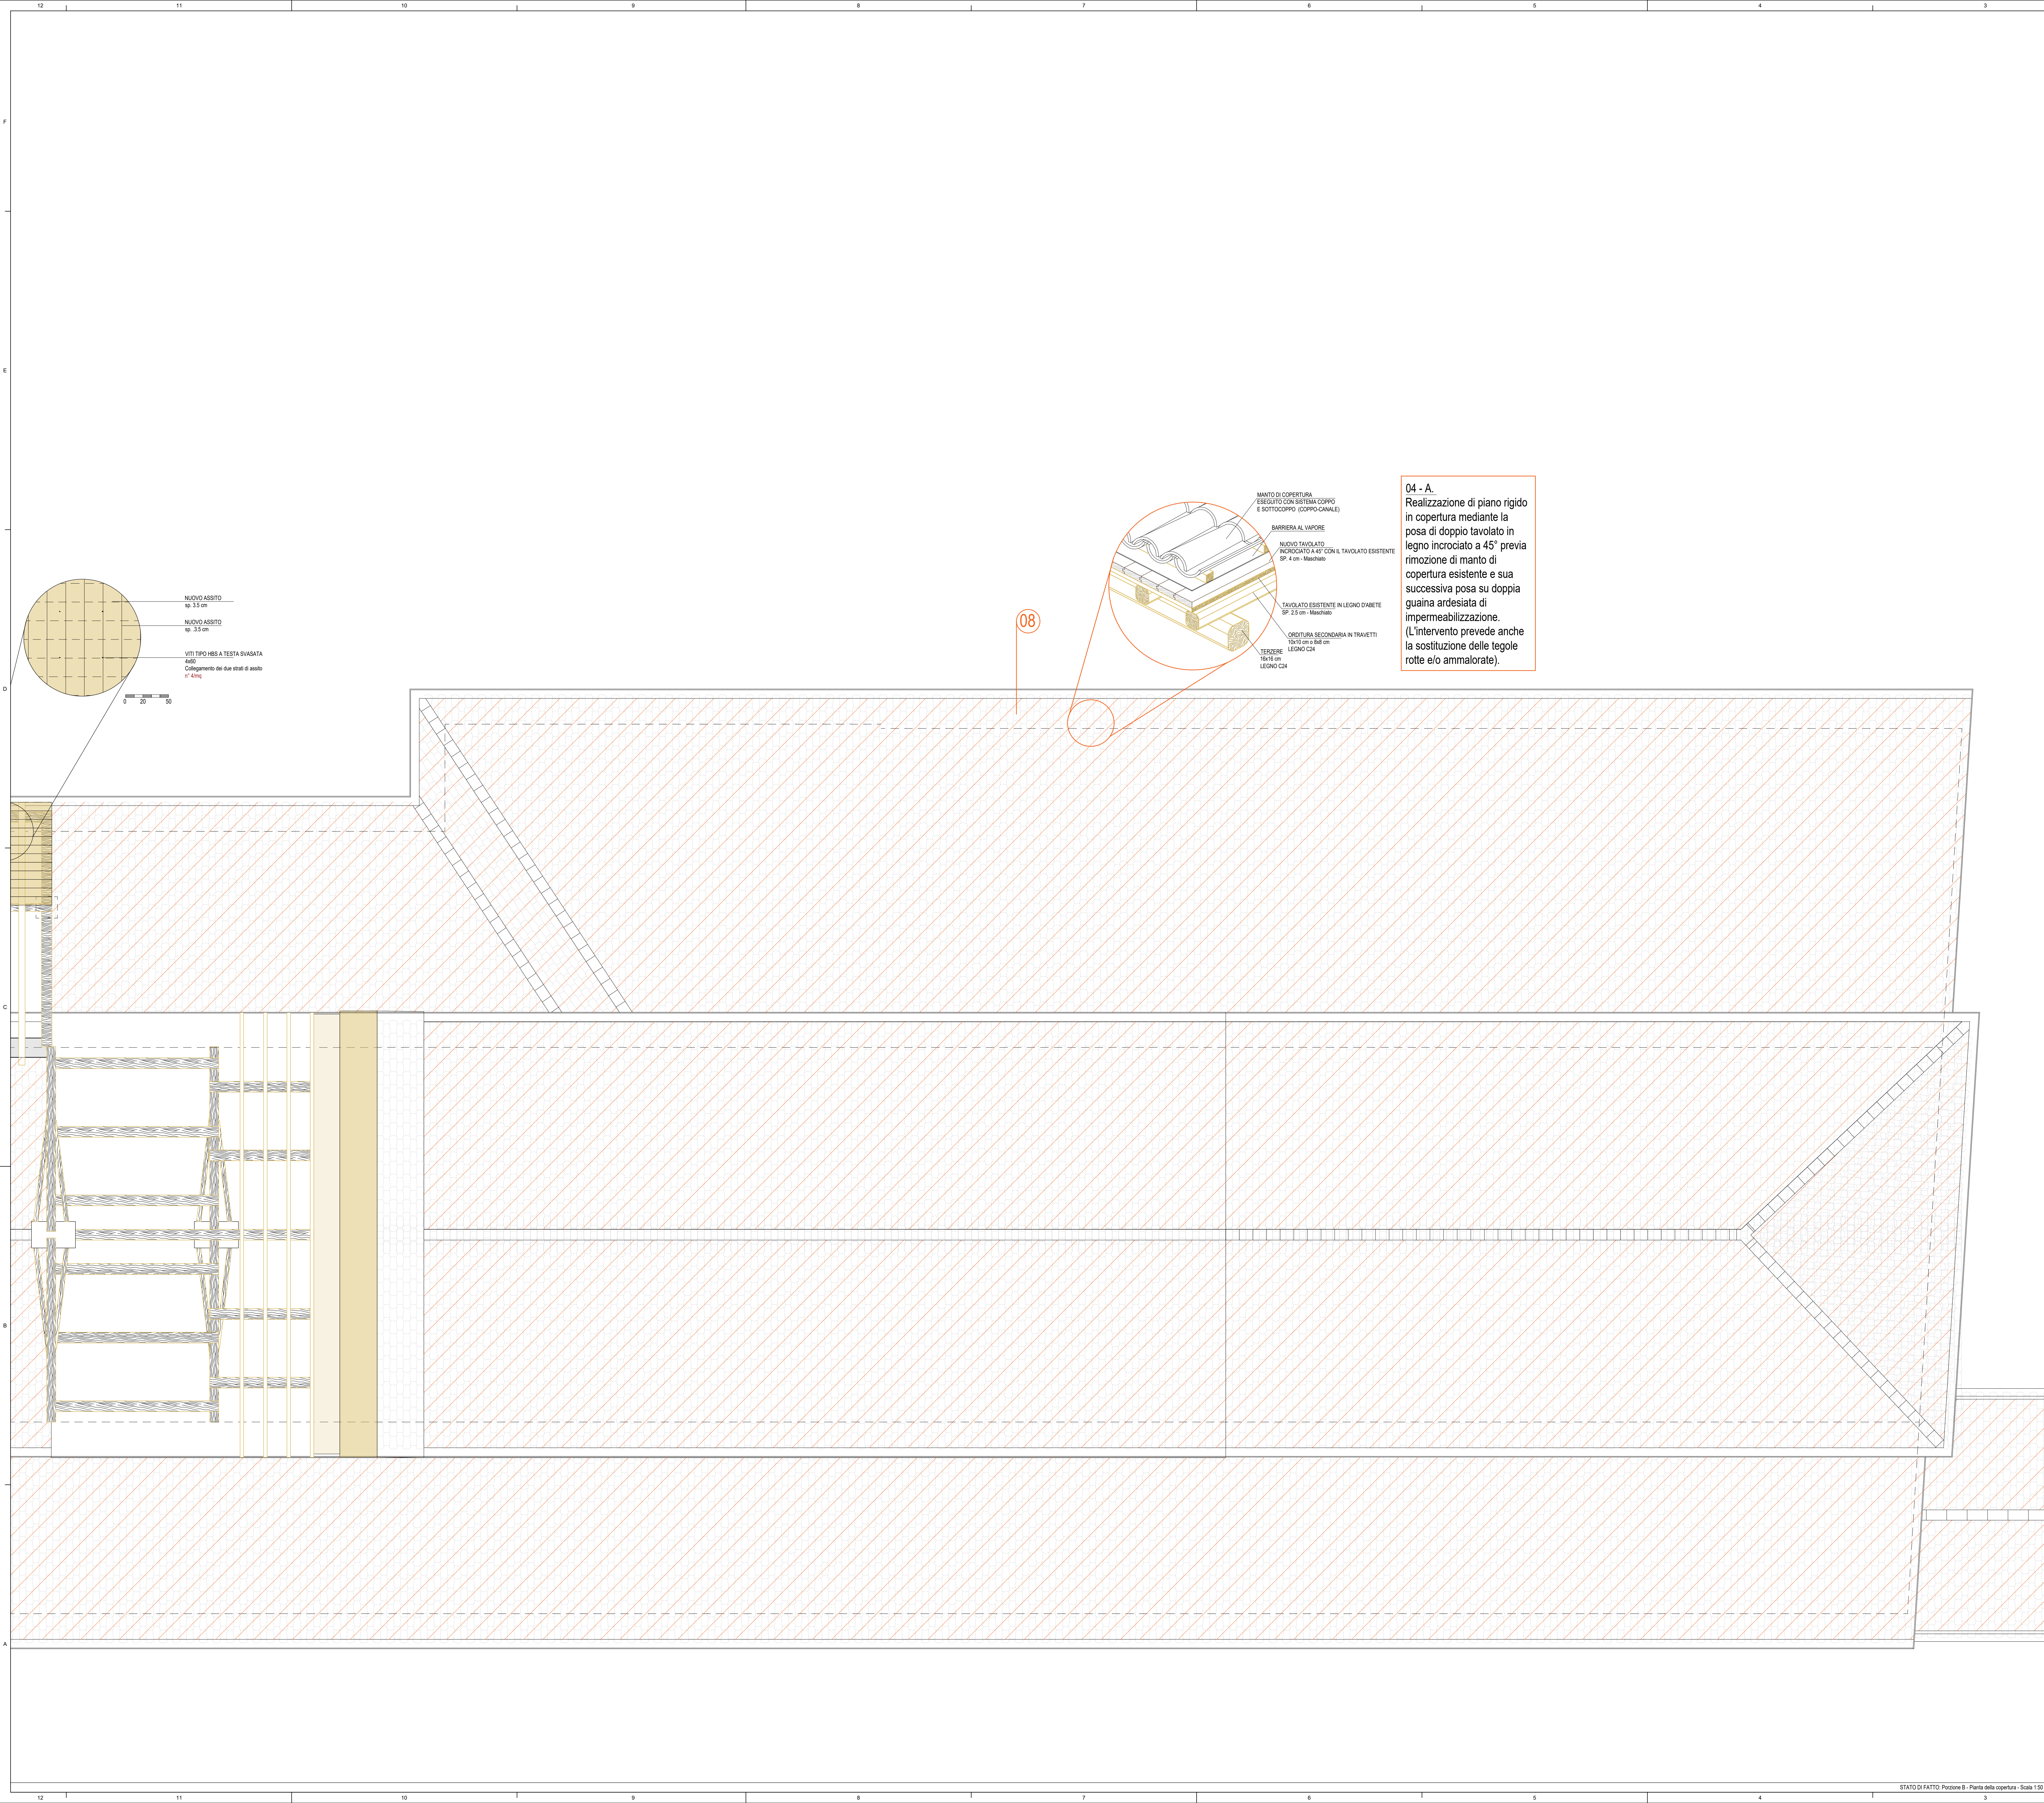


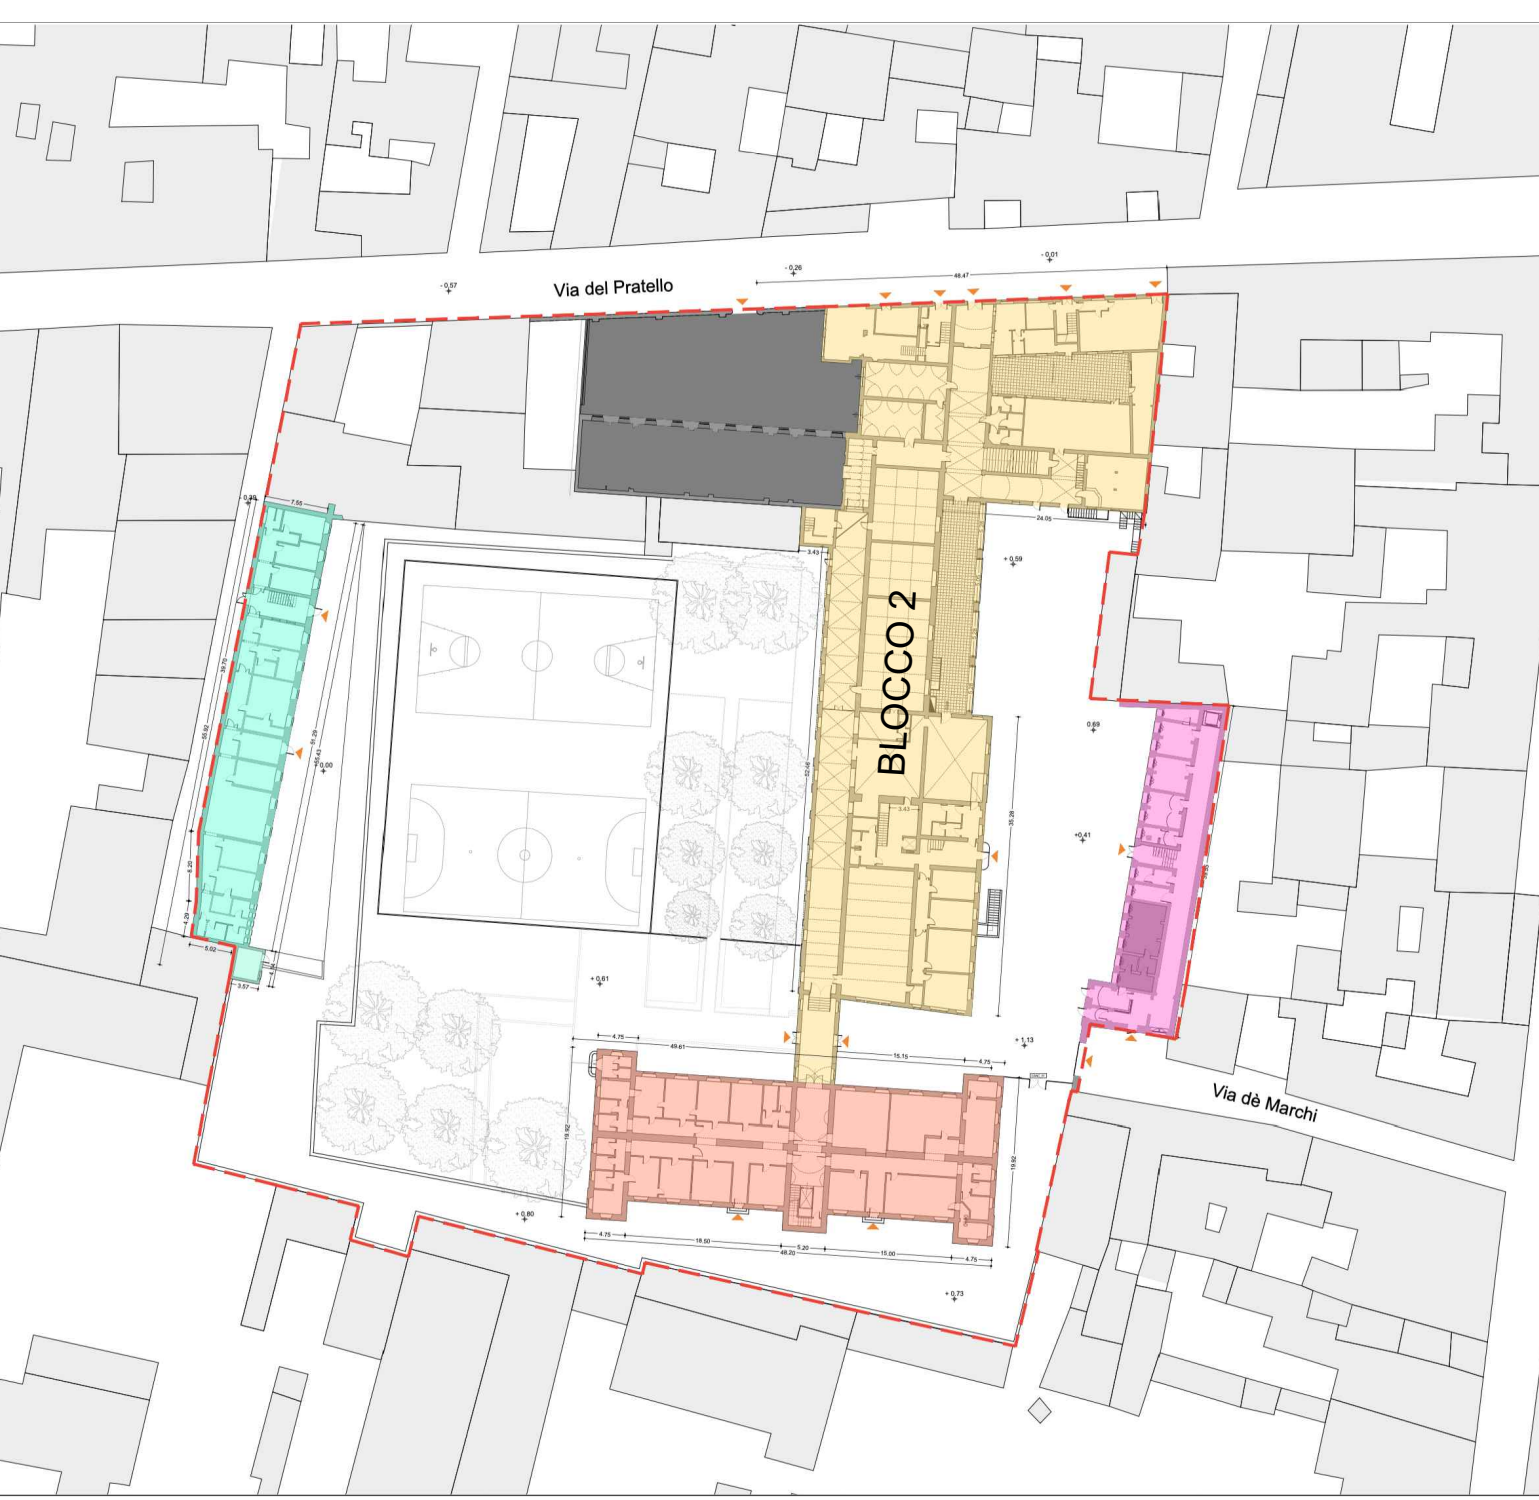

TIPOLOGIA DI INTERVENTO	LEGENDA DEGLI INTERVENTI	LEGENDA DEI RETINI	
		MURATURA PORTANTE	
D1. FASCE IN FIBRA DI ACCIAIO (INTONACO ARMATO)		TRAVESSE ESISTENTI	
D2. INTERVENTO SU MURATURE A SACCO (INTONACO ARMATO)		NUOVI TRAVEZZI REALIZZATI SECONDO INDICAZIONI UNITARI	
D3. FASCE IN FIBRA DI ACCIAIO APPLICATE SU UN SINGOLO LATO (INTONACO ARMATO)		PORTAZIONI DI TRAVEZZI DA DEMOLIRE E RICOSTRUIRE PER CONSERVARE LA CONTINUITÀ DELL'INTONACO ARMATO	
D4. CERCCHIATURA DEI PILASTRI		CHIUSURA DELLA NICHIA ESISTENTE CON MURATURA PORTANTE (MATTONE PIENO E MALTA DI CALCE MIO)	
D5. GIUNTO BERNINI			
D6. CATENE IN ACCIAIO			
D7. FASCE DI PIANO DI BICO ARMATO (o simili)			
D8. PIANO RIGIDO IN COPERTURA			

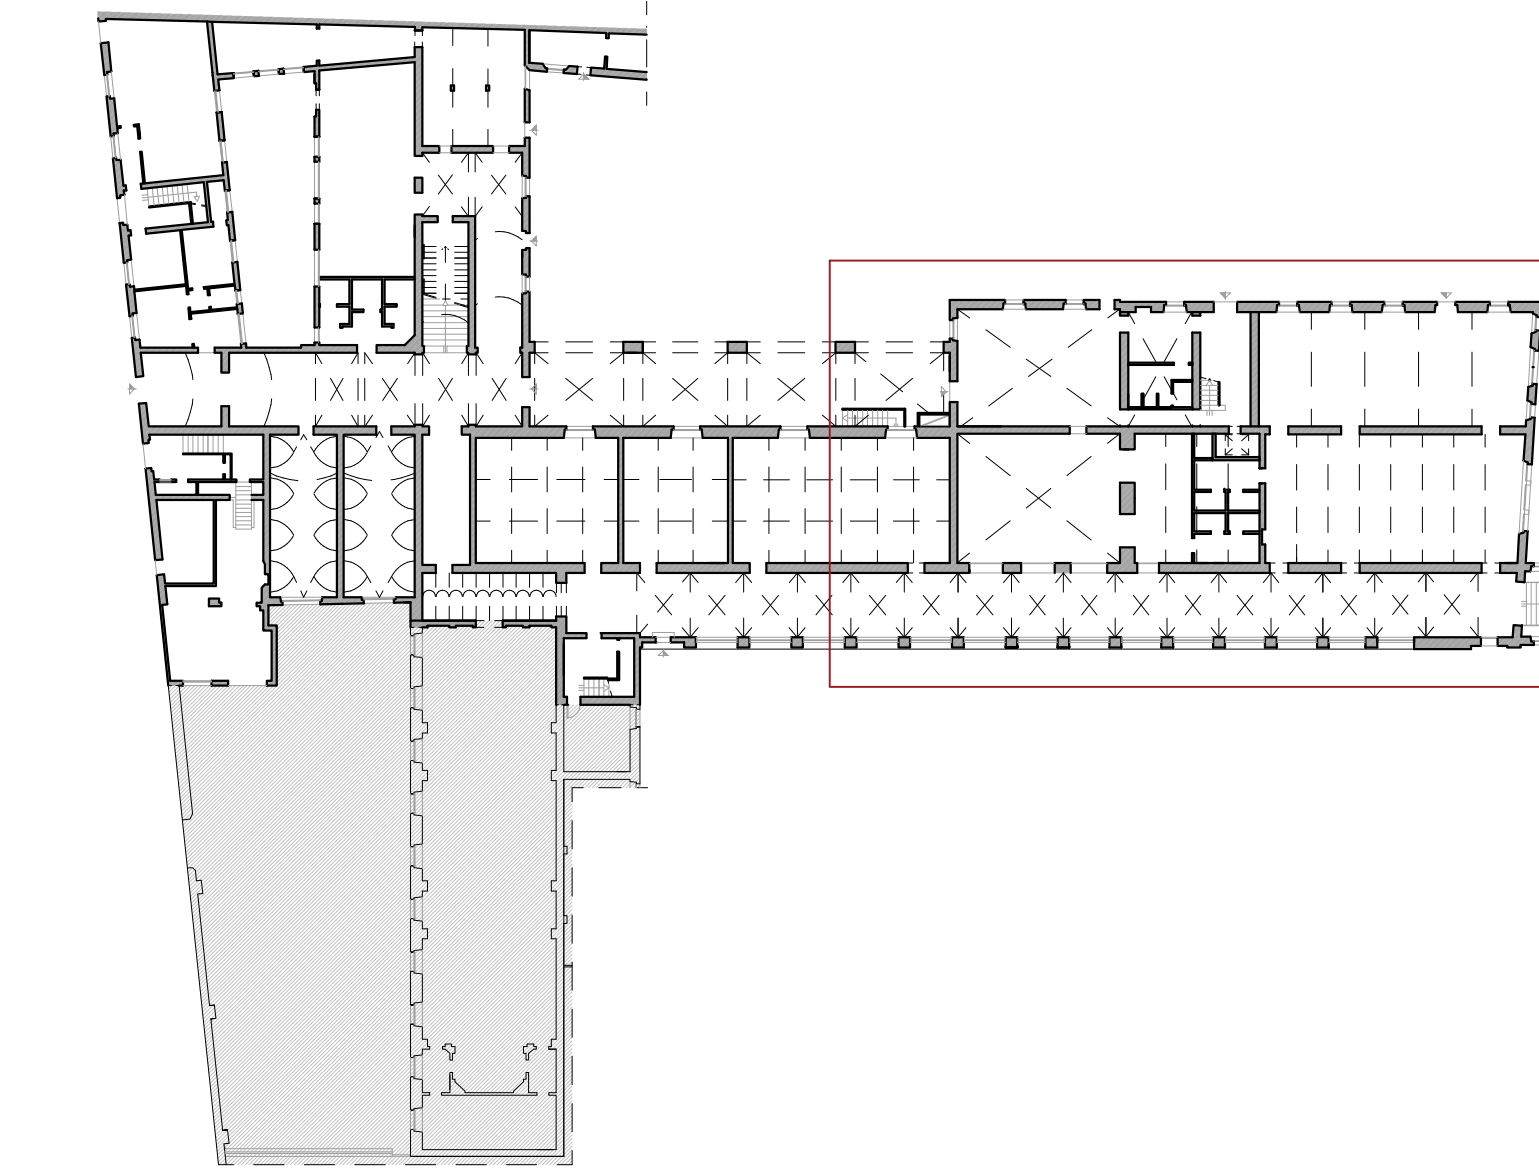

Ministero delle Infrastrutture e dei Trasporti

Provveditorato Interregionale per le Opere Pubbliche Lombardia e Emilia Romagna
sede coordinata di Bologna - Piazza VIII Agosto, 26 - 40126 BOLOGNA

974-PNC - BO 7322 - Affidamento della progettazione esecutiva ed esecuzione lavori per gli interventi di miglioramento sismico, efficientamento energetico ed adeguamento funzionale del carcere minorile in Via del Pratello a Bologna.
CUP D39J21022100006 CIG B2373792CA

IL RESPONSABILE UNICO DEL PROCEDIMENTO

Dott. Ing. Roberto GAMBARTO

IL DIRETTORE DELL'ESECUZIONE DEL CONTRATTO

Dott. Ing. Roberto GAMBARTO

Progettista incarico

Progettista responsabile dell'integrazione tra le varie prestazioni specialistiche: [Arch. Paolo Menichetti](#)

Progettista responsabile progetto strutturale: [Arch. Paolo Menichetti](#)

Progettista responsabile progetto impiantistico: [Arch. Paolo Menichetti](#)

Consulente impianti: P.I. Eligio Dotti

Studio AARC.it
Via Giuseppe Mazzini 32
51122 Livorno (LI)

SICEA
Via Belforte, 8
33010 Vigonza (PD)

Disciplina di progetto:

ELABORATI STRUTTURALI
PROGETTO ESECUTIVO
PROGETTO - Blocco 2 - Pianta Copertura Zona B e dettagli costruttivi
PE 2S.2.PG.PWT.222.00

SCALA 1:50

DATA 02/12/2024

STATO DI FATTO Posizione B - Pianta della copertura - Scala 1:50