

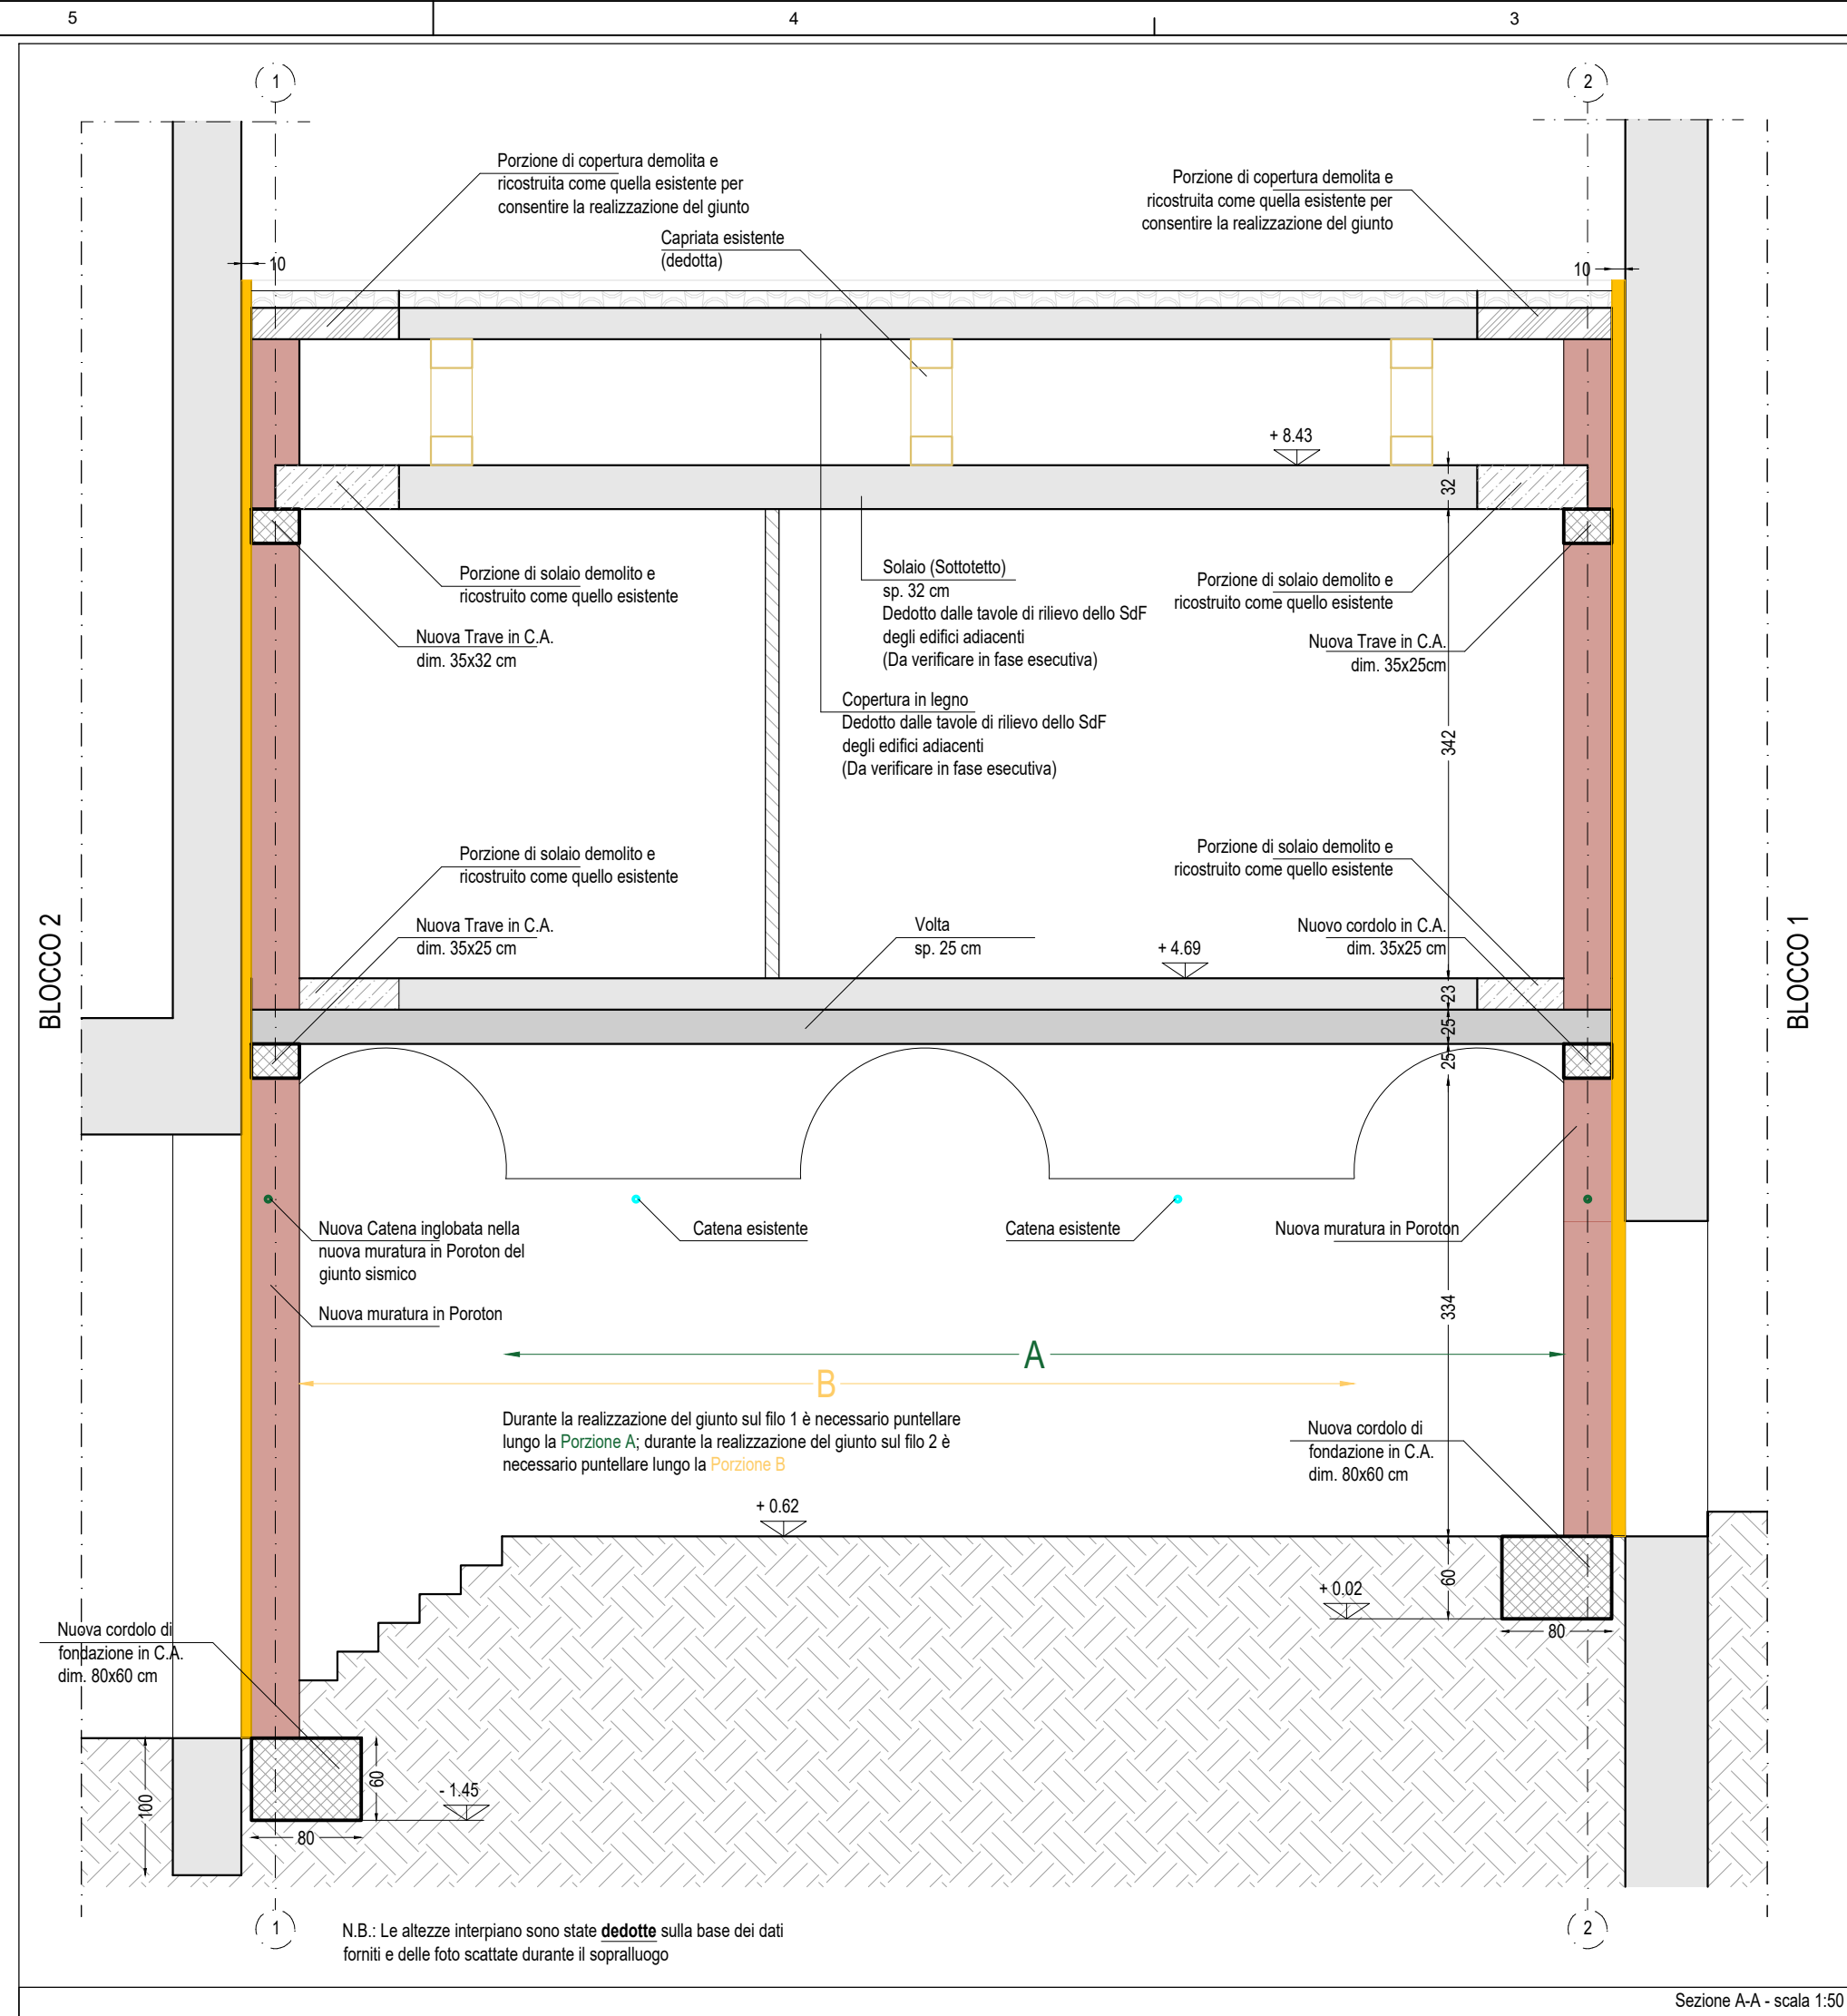
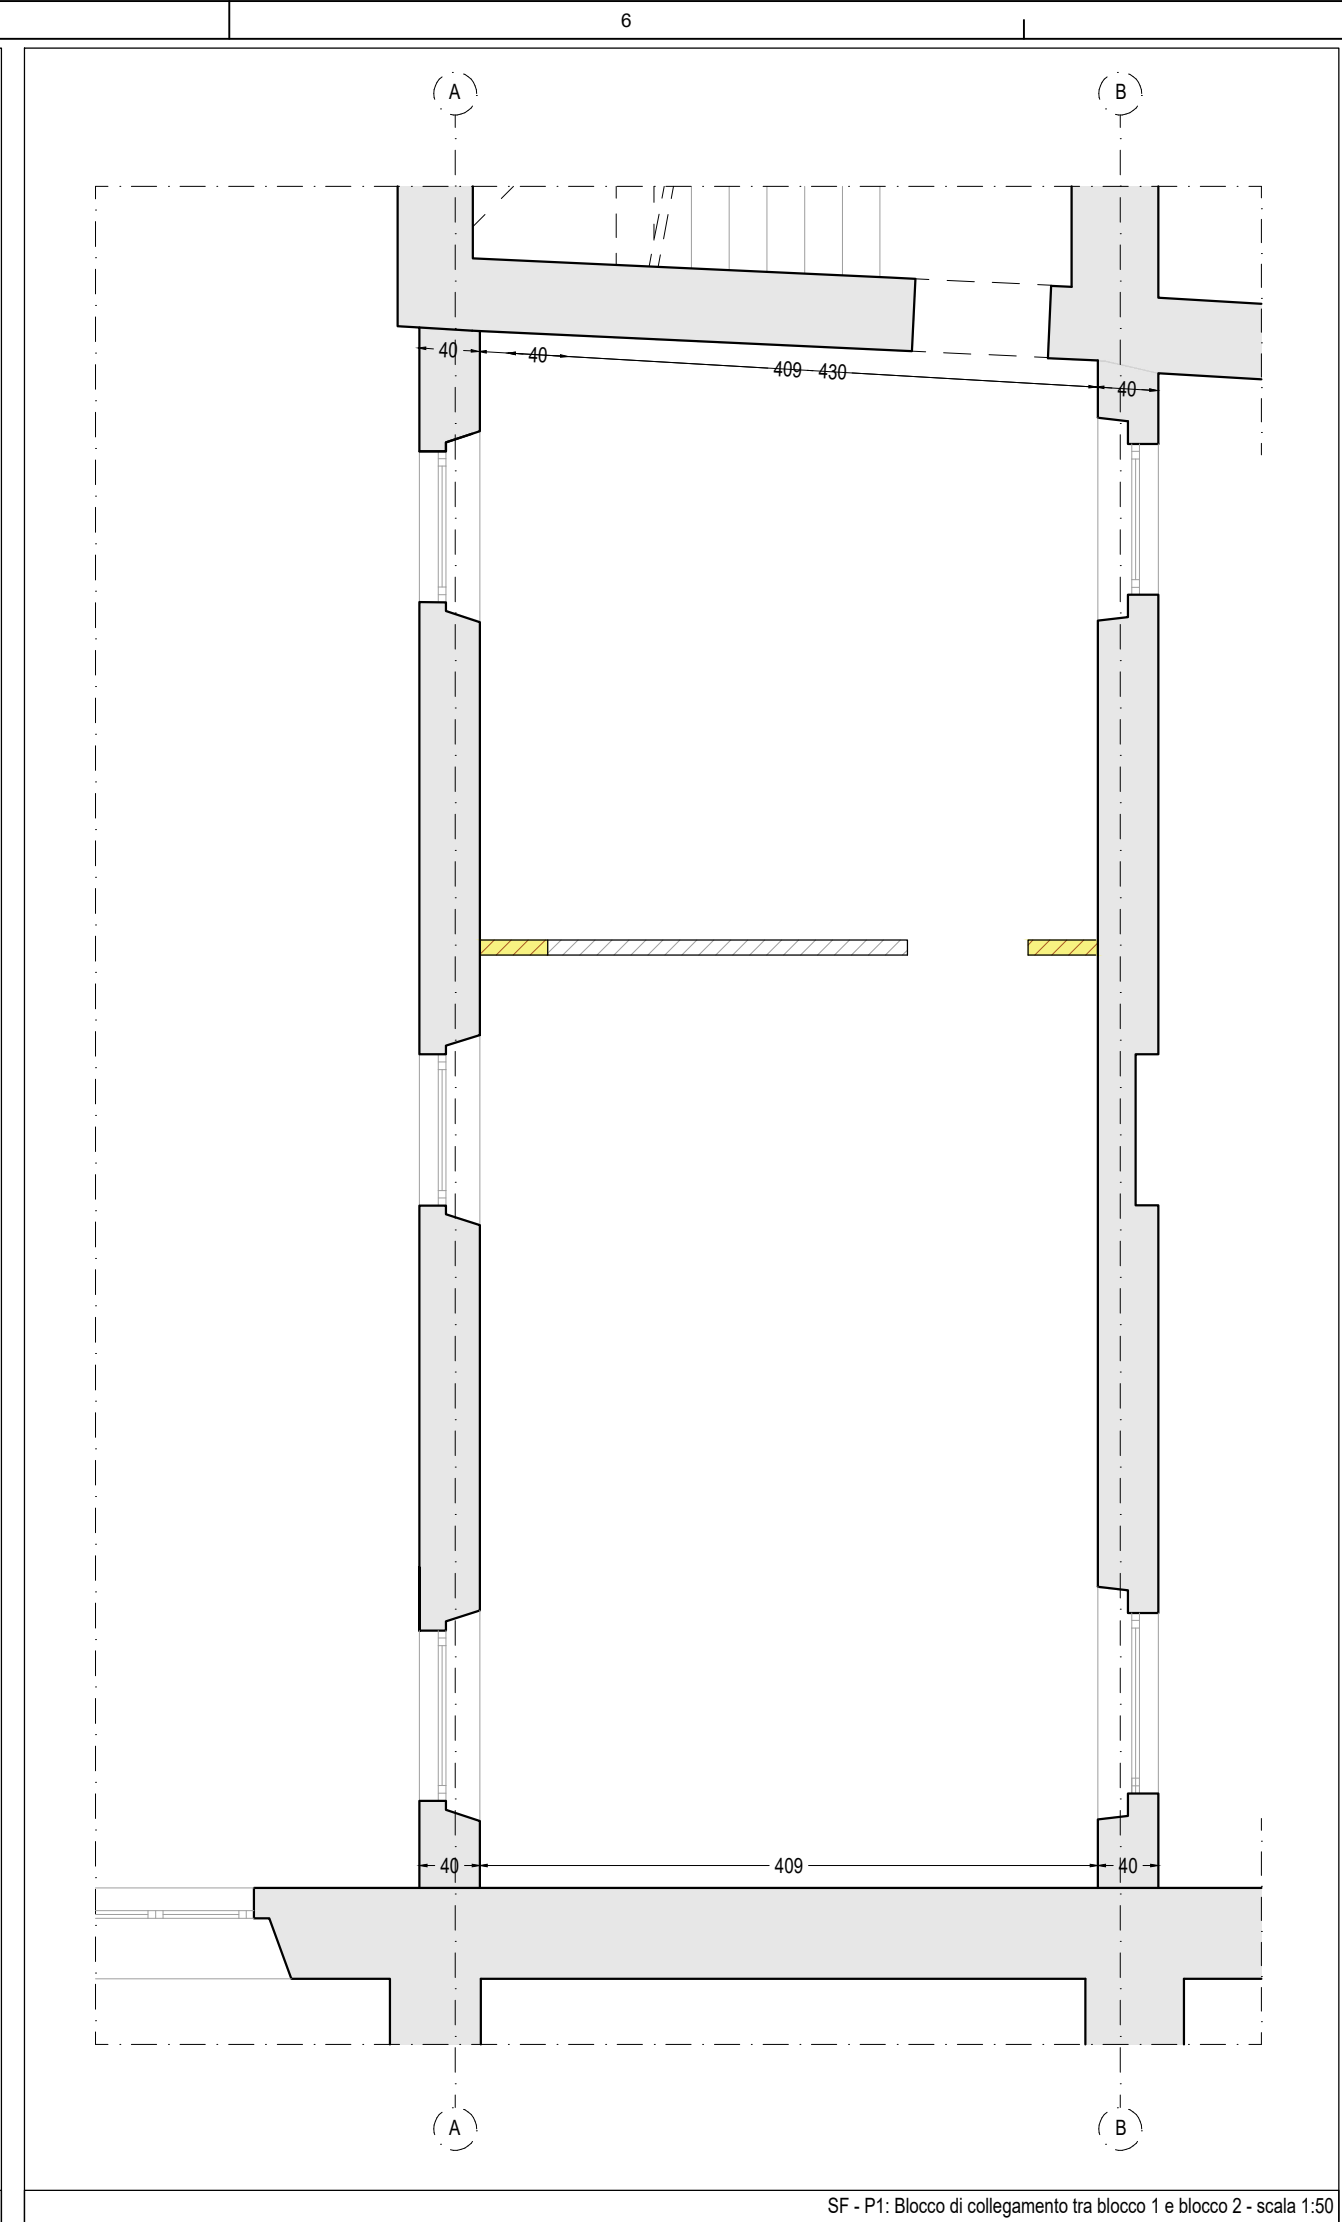
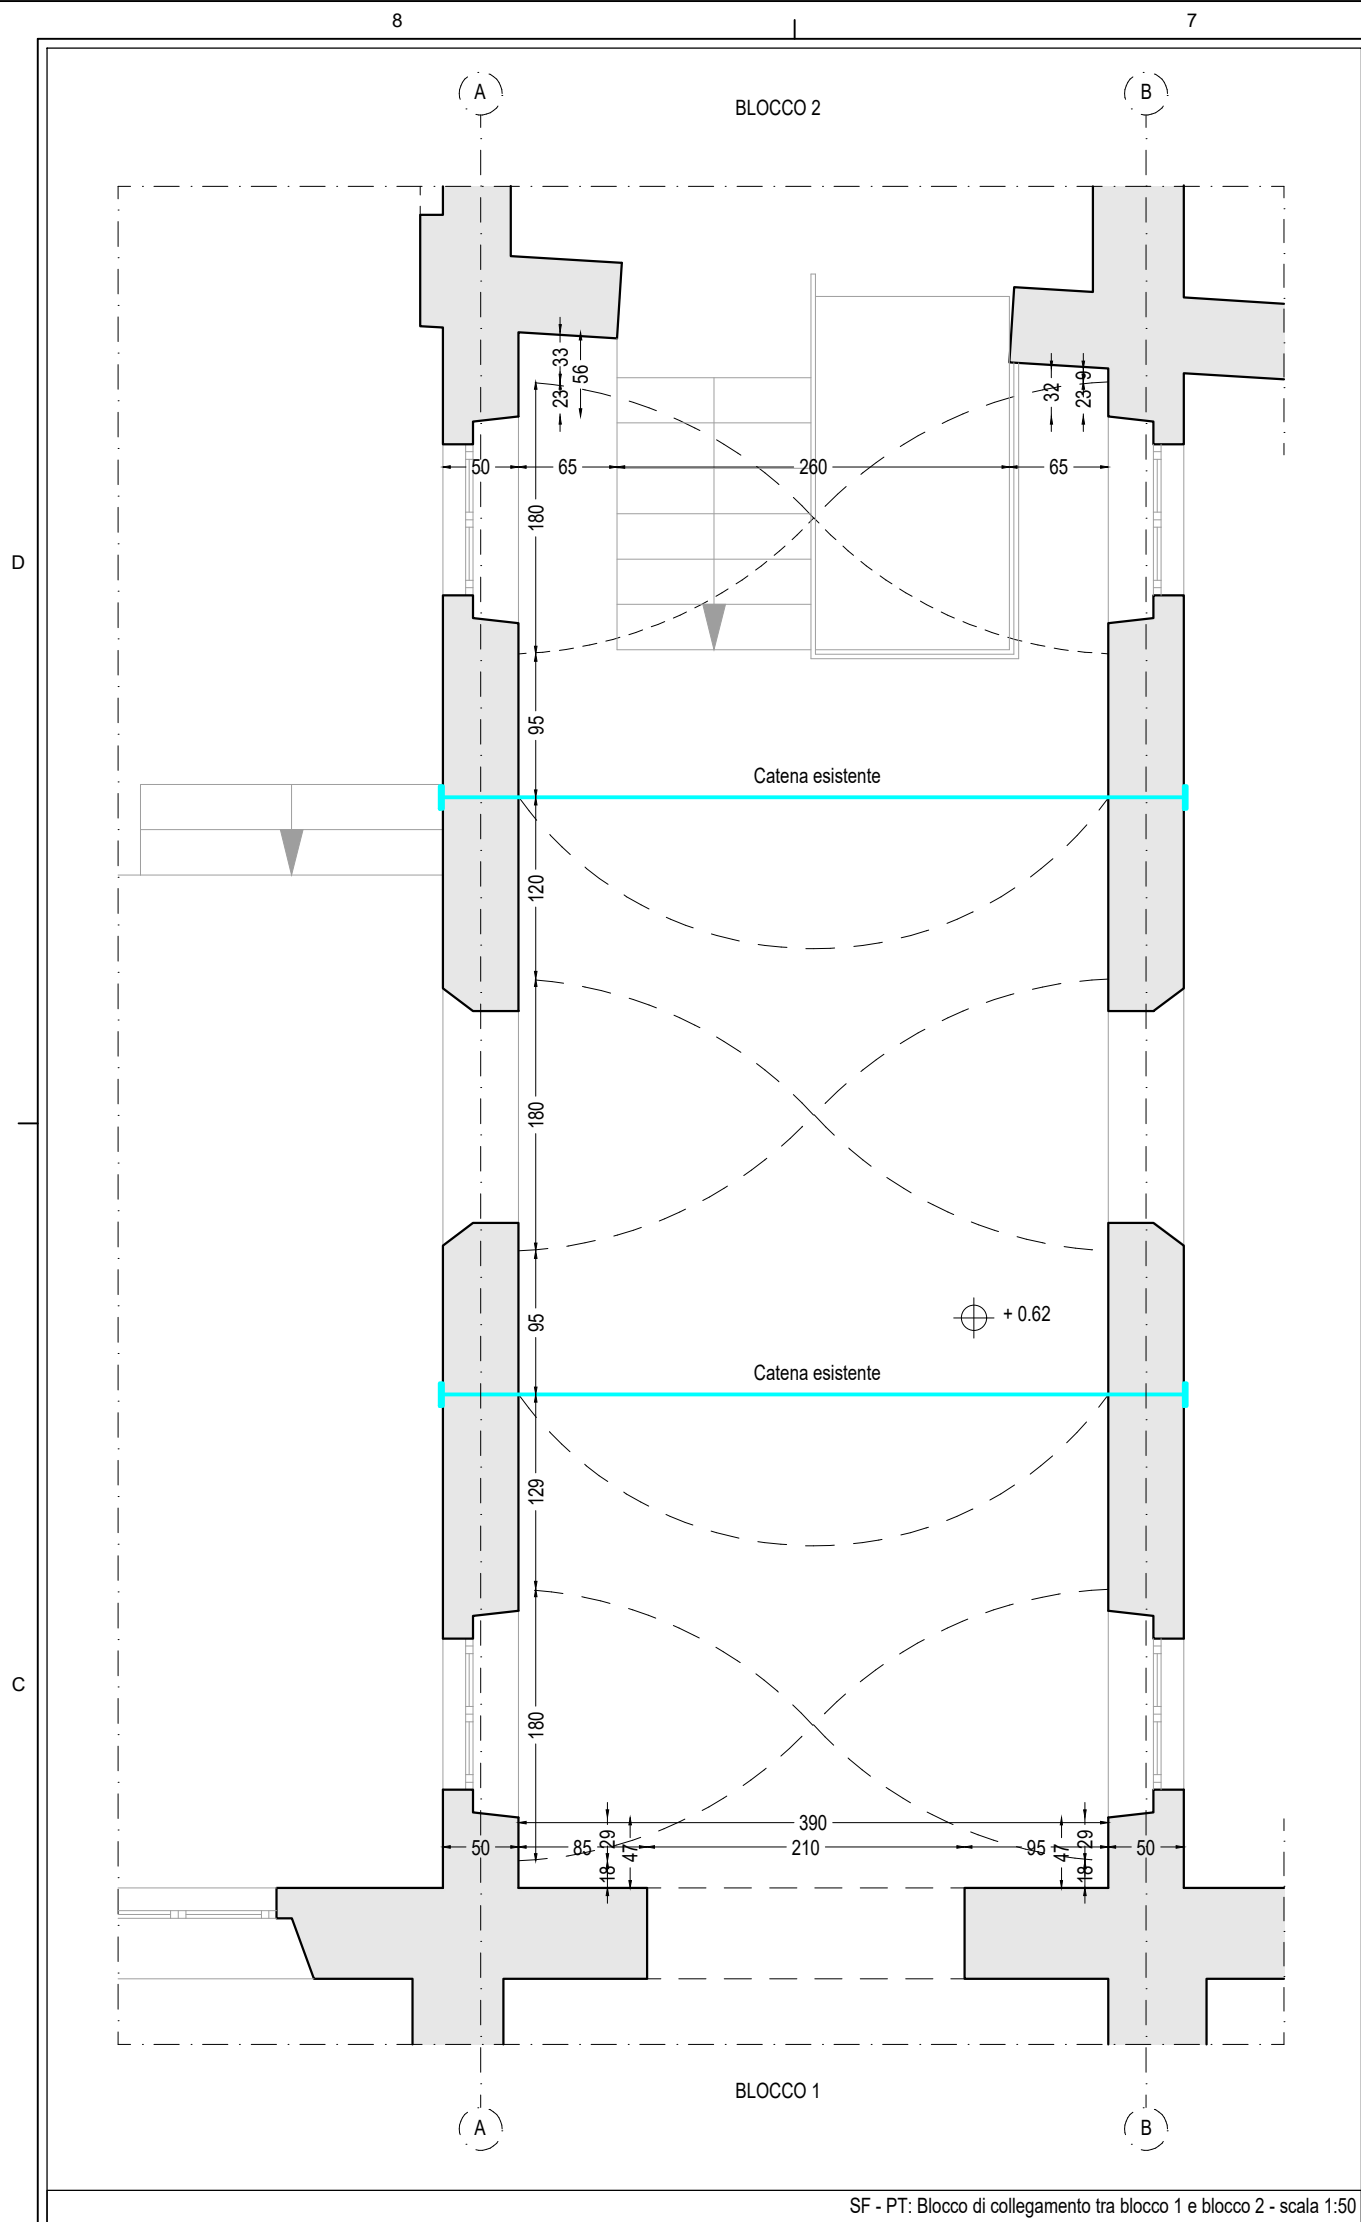
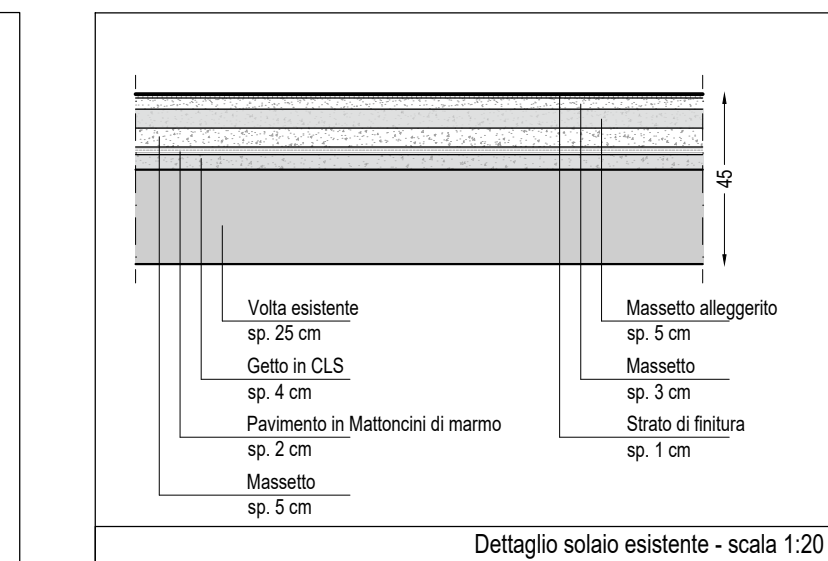
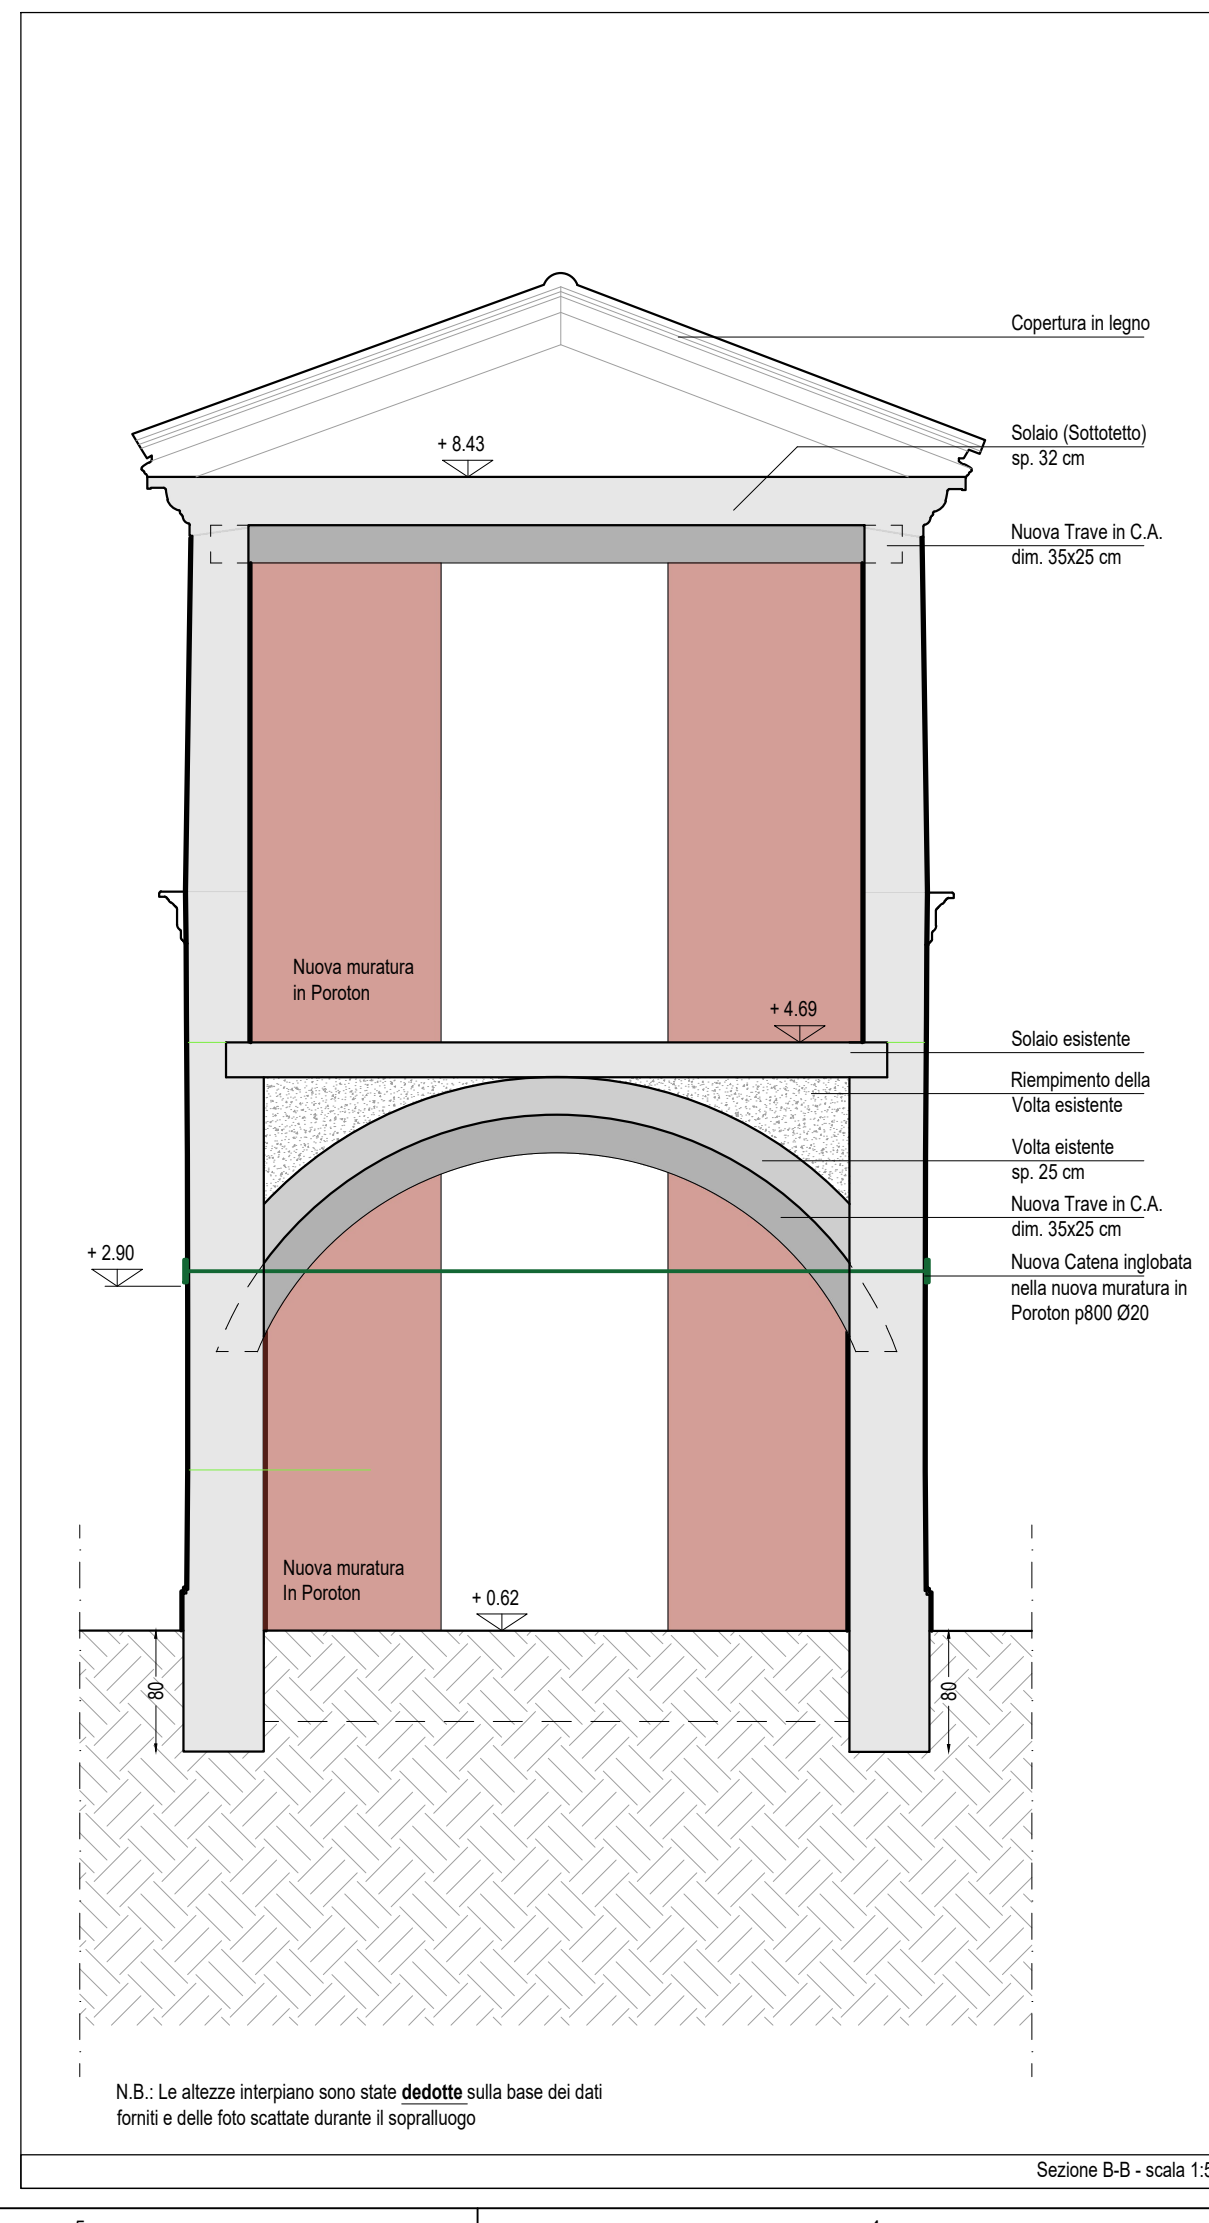
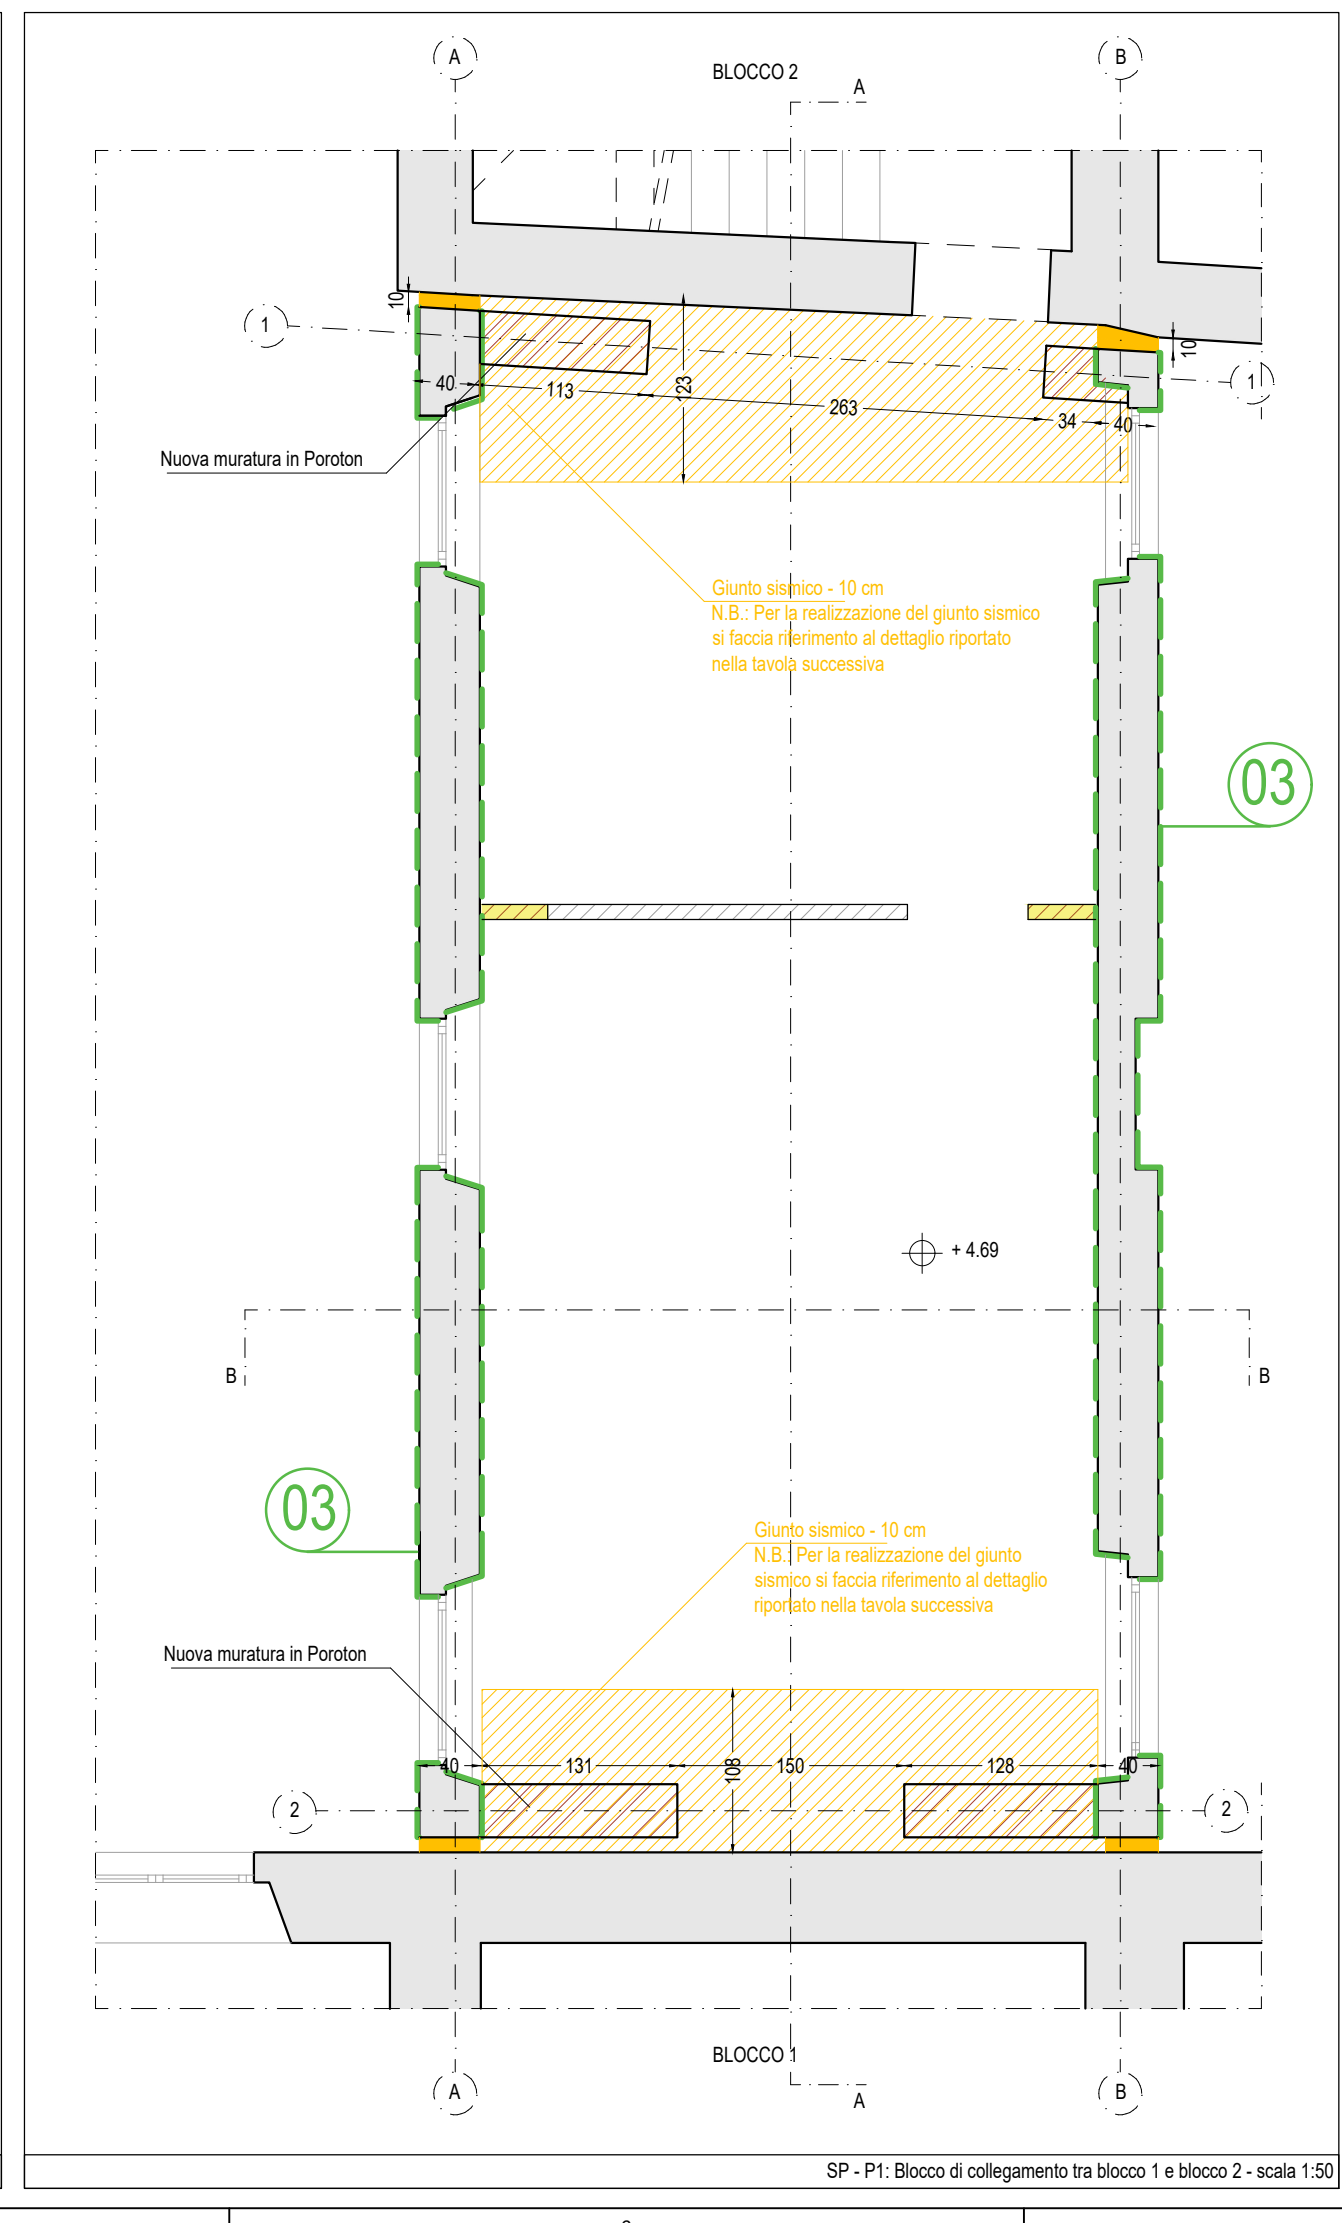


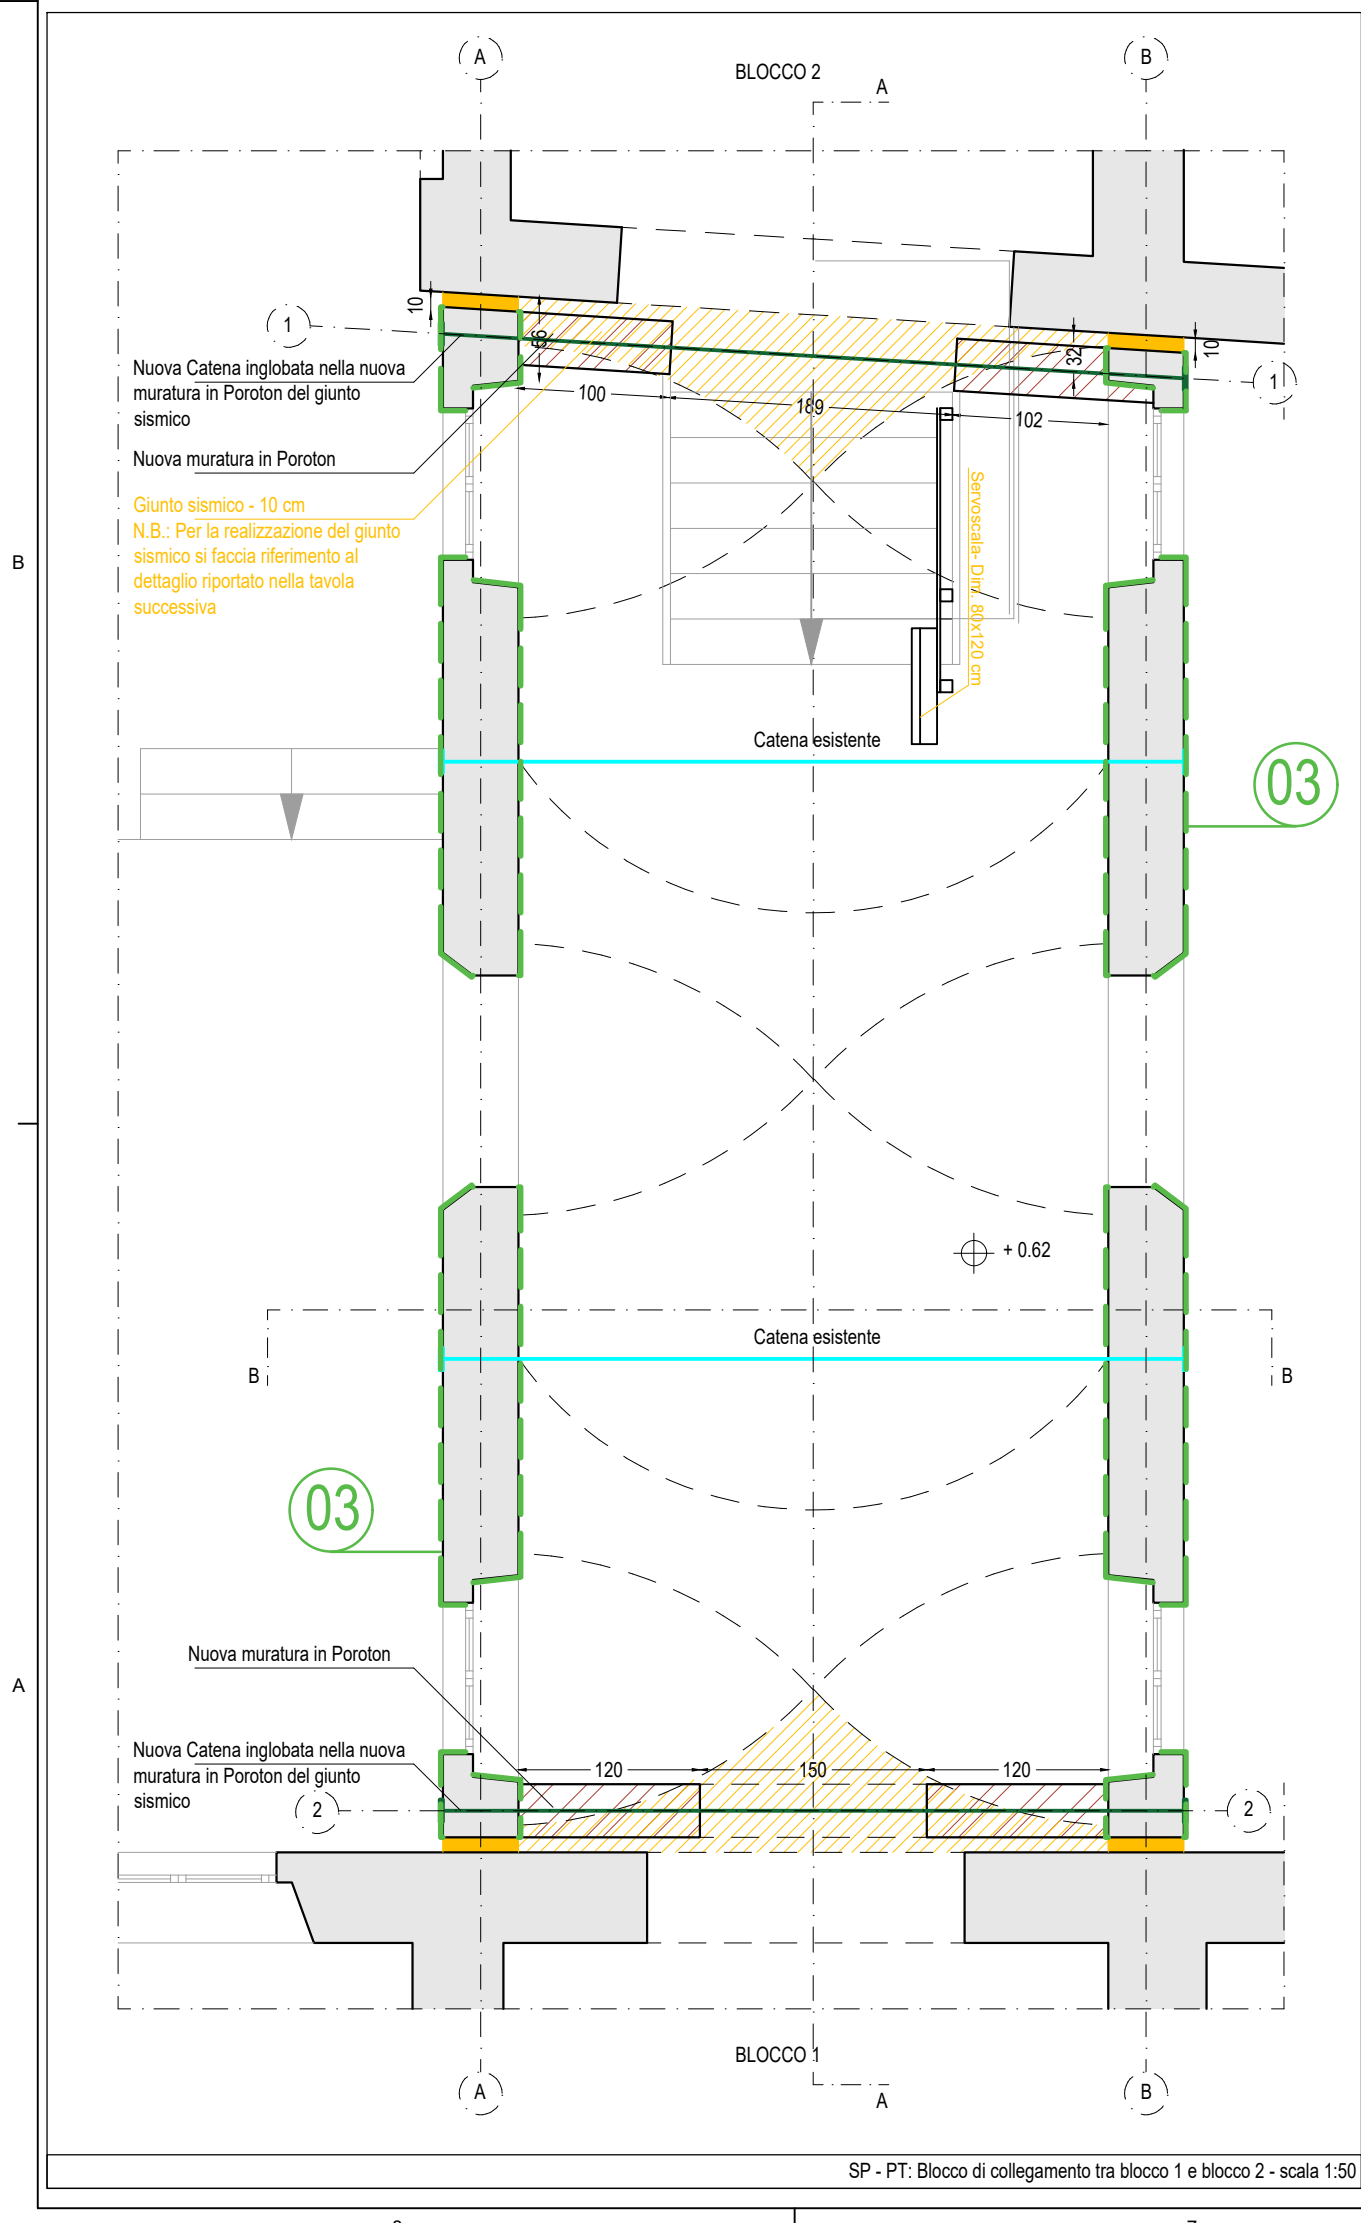

TIPOLOGIA DI INTERVENTO	LEGENDA DEGLI INTERVENTI	LEGENDA DEI RETINI
01. GIUNTO SISMICO Demolizione di un'azione della parete esistente (sp. 10 cm) e del solaio interpiano e di copertura in modo da rendere indipendenti le strutture dei blocchi 1 e 2 dal blocco di collegamento tra essi.		MURATURA PORTANTE
02. NUOVA CATENA IN ACCIAIO Inserimento di una catena in acciaio con elemento di collegamento tra due muri tra loro paralleli		TRAMEZZI ESISTENTI
03. FASCE IN FIBRA DI ACCIAIO (INTONACO ARMATO) Rinforzo dei maschi murari esistenti mediante la posa di intonaco armato diffuso		PORZIONI DI TRAMEZZI DA DEMOLIRE E RICOSTRUIRE PER CONSENTIRE LA CONTINUITÀ DELL'INTONACO ARMATO
		NUOVI MURATURA ARMATA REALIZZATA IN POROTON P800 - A CHIUSURA DELLE PORZIONI DEMOLITE PER LA CREAZIONE DEL GIUNTO
		NUOVO CORDOLO IN C.A.
		SEZIONATO IN VISTA
		SEZIONATO IN VISTA

NOTA:
PRIMA DELLA DEMOLIZIONE PER LA REALIZZAZIONE DEL GIUNTO SISMICO È NECESSARIO PUNTELLARE L'INTERO CAMPO DI SOLAIO INDICATO PREVIA APPROVAZIONE DELLO SCHEMA DI PUNTELLAMENTO DA PARTE DELLA DL STRUTTURE.
CONFERMARE QUANTO DESUNTO DA RILIEVI BLOCCHI ADIACENTI SU VOLTA E COPERTURA IN LEGNO
CONFERMARE LE QUOTE IN QUANTO DESUNTE DA RILIEVI ADIACENTI.

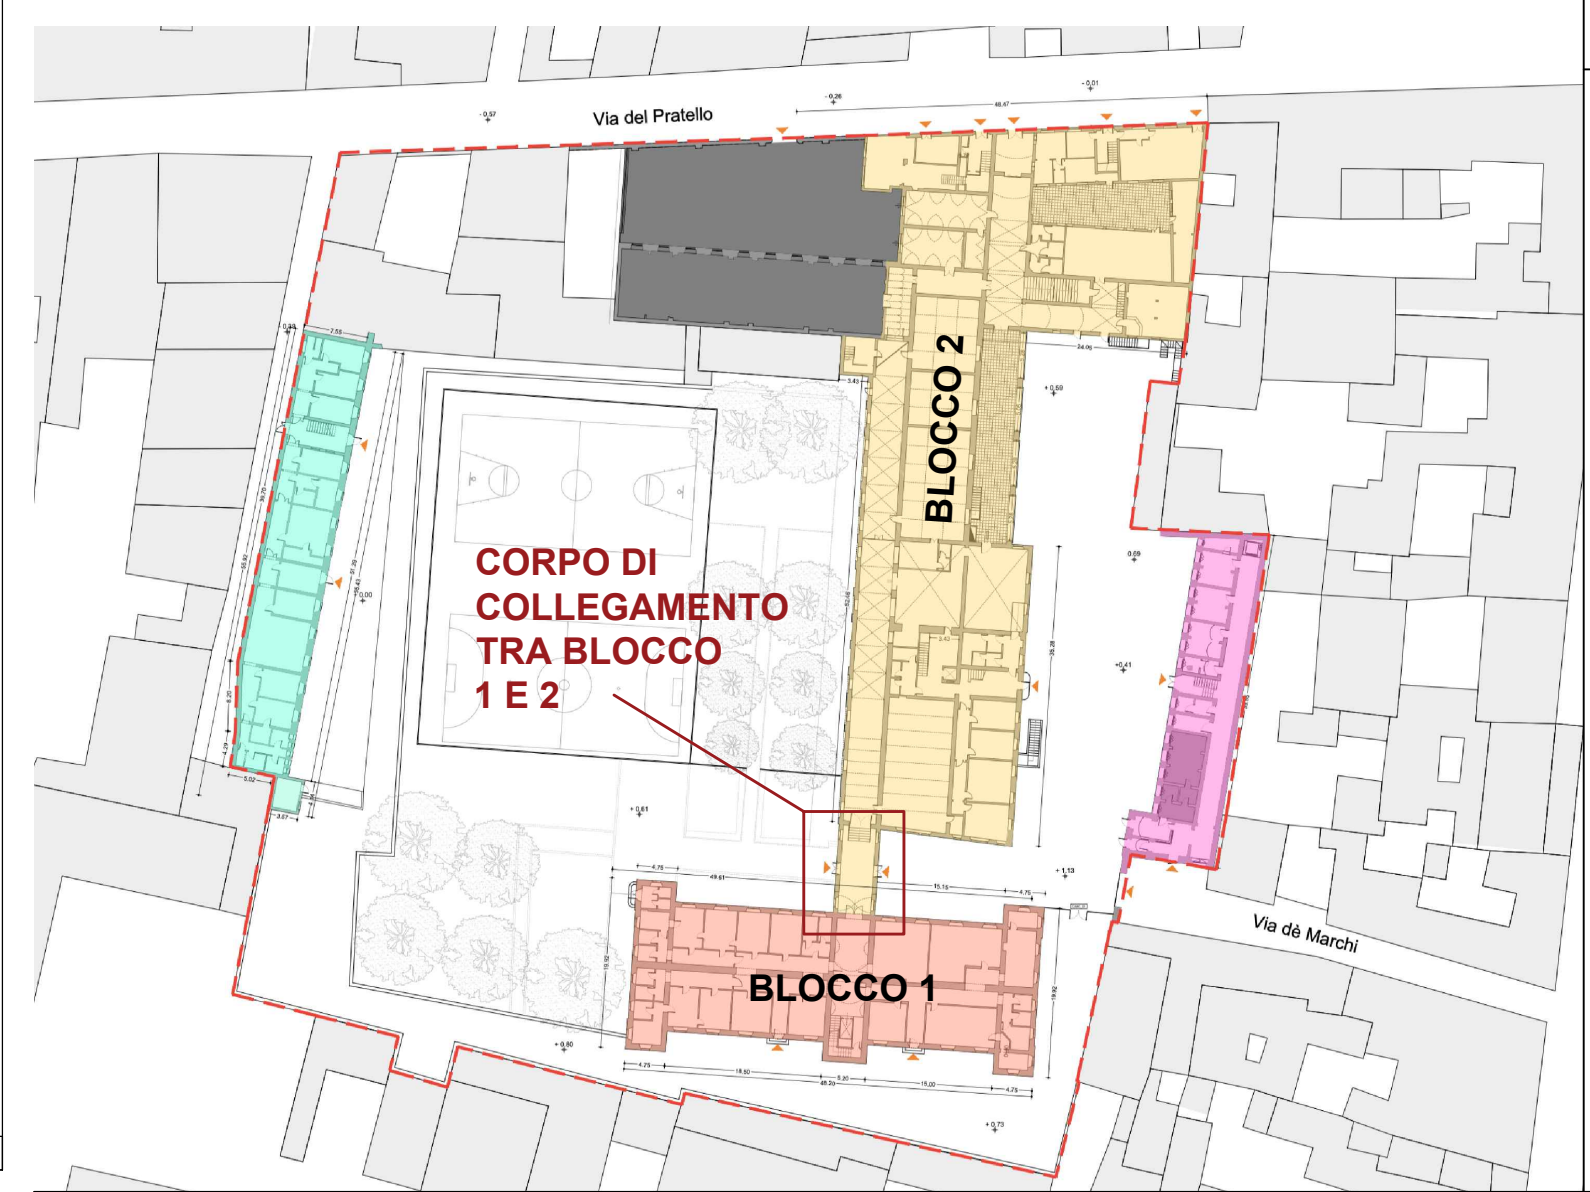

Finanziato dall'Unione europea NextGenerationEU

Ministero delle infrastrutture e dei trasporti

Ministero delle Infrastrutture e dei Trasporti

Provveditorato Interregionale per le Opere Pubbliche Lombardia e Emilia Romagna

sede coordinata di Bologna - Piazza VIII Agosto, 26 - 40126 BOLOGNA

974-PNC - BO 73/22 - Affidamento della progettazione esecutiva ed esecuzione lavori per gli interventi di miglioramento sismico, efficientamento energetico ed adeguamento funzionale del carcere minorile in Via del Pratello a Bologna.

CUP D39J21022100006 CIG B2373792CA

IL RESPONSABILE UNICO DEL PROCEDIMENTO

Dott. Ing. Roberto GAMBAROTA

IL DIRETTORE DELL'ESECUZIONE DEL CONTRATTO

Progettisti indicati

Progettista responsabile dell'integrazione tra le varie prestazioni specialistiche: Arch. Dario Menichetti

Progettista responsabile progetto architettonico: Arch. Valentina Menichini

Progettista responsabile progetto strutturale: Arch. Dario Menichetti

Progettista responsabile progetto impianti: Arch. Dario Menichetti

Consulente impianti: P.I. Eligio Dati

AARC.it

CONTRAENTE

SICEA

Studio AARC.it

Via Giuseppe Maria Terenzi 32

57122 Livorno (LI)

SICEA

Via Bachelet, 8

35010 Vigonza (PD)

Disciplina di progetto:

ELABORATI STRUTTURALI

PROGETTO ESECUTIVO

Giunto sismico del corpo tra Blocco 1 e Blocco 2: Pianta dello SdF, Pianta dello SdF, Sezione AA e Sezione BB

PE.2S.1-2.POP1.PNT-SEZ.212.00

SCALA Varie

DATA 02/12/2024

Nome file:

Questo elaborato è di proprietà del Ministero delle Infrastrutture e delle Mobilità Sostenibili non può essere riprodotto, anche parzialmente, senza autorizzazione