

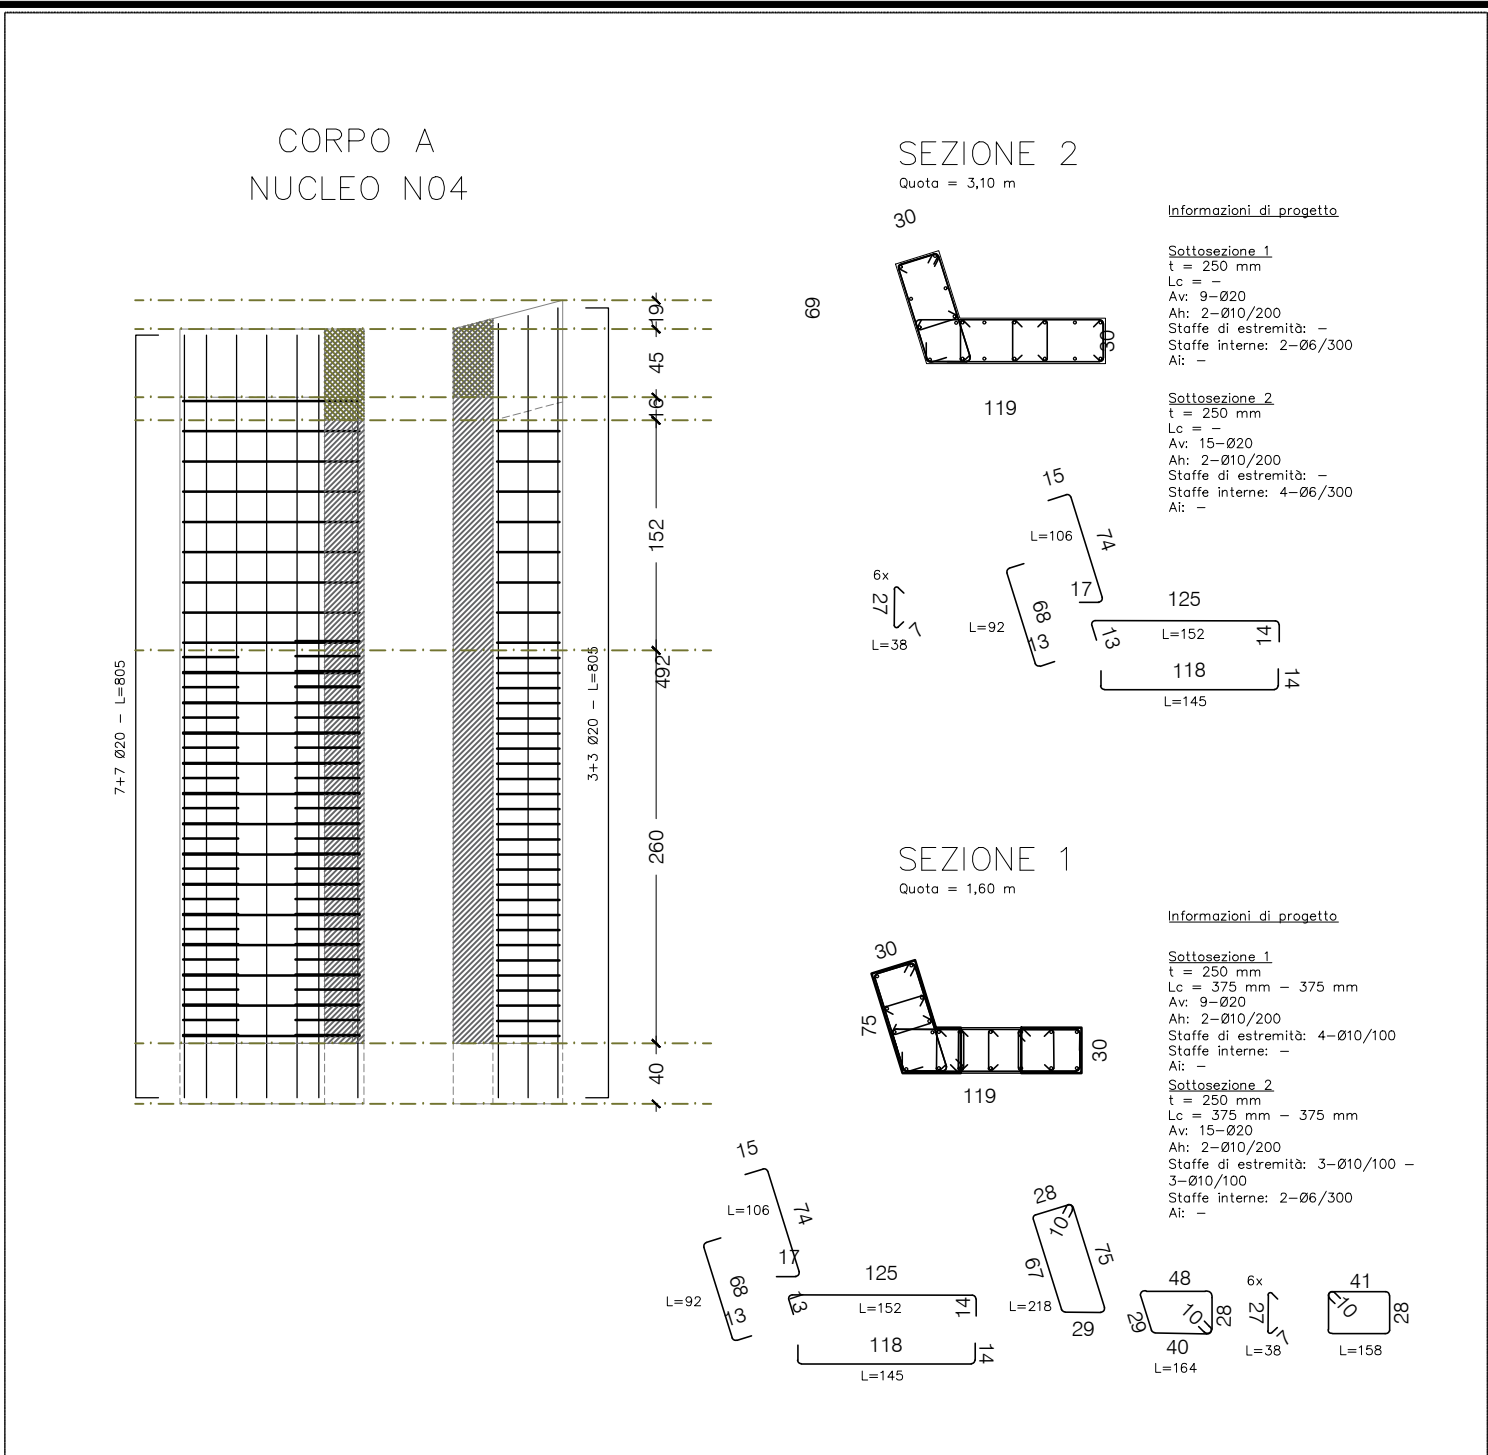
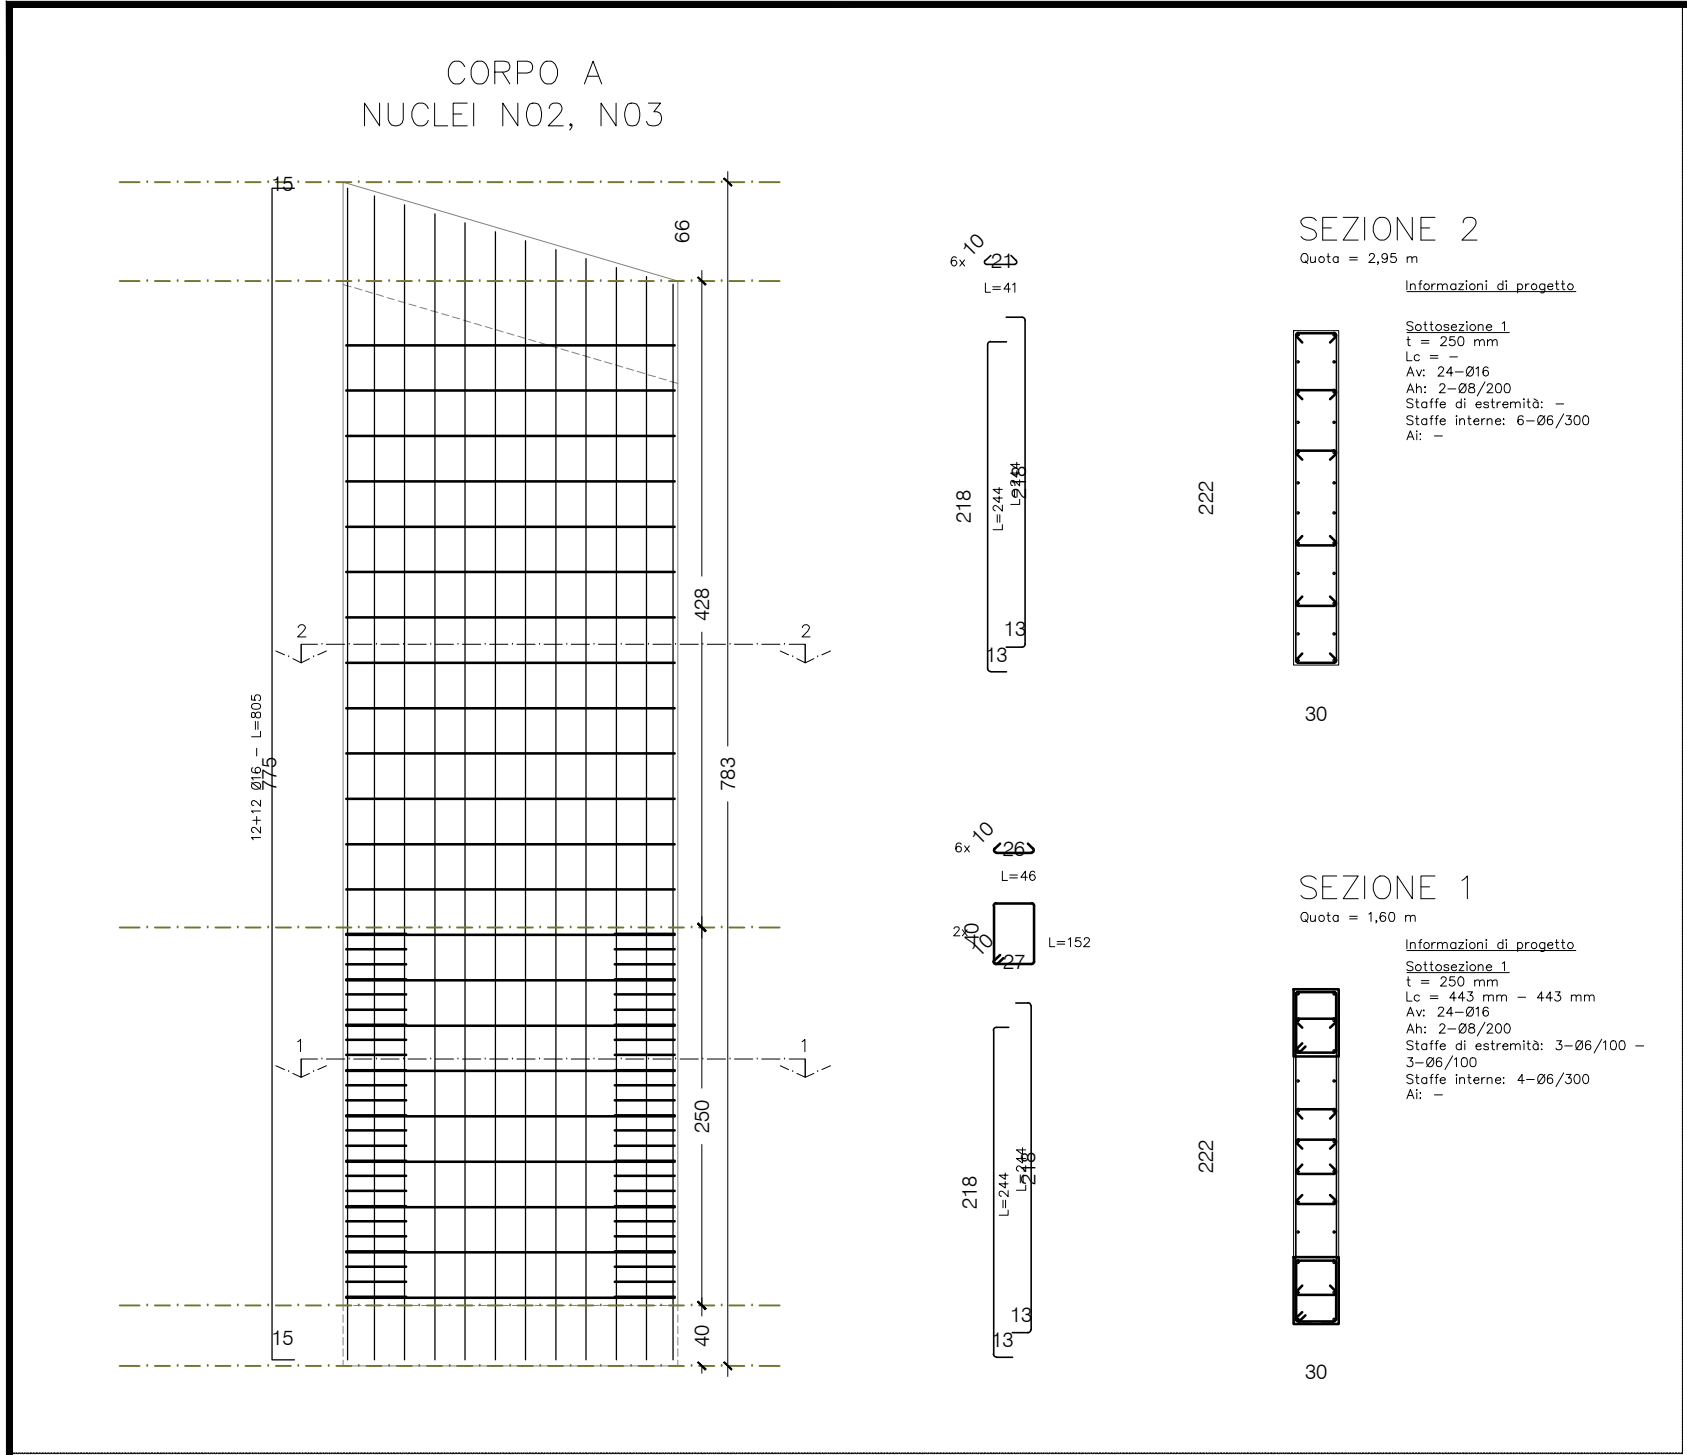
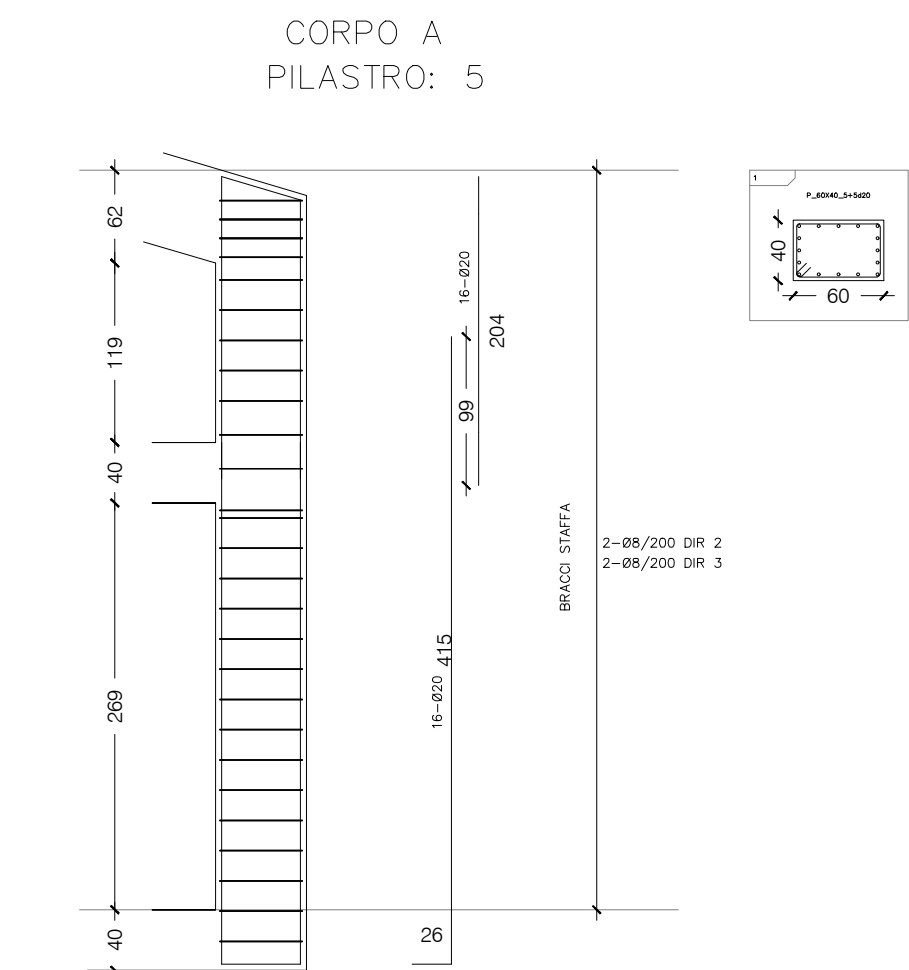
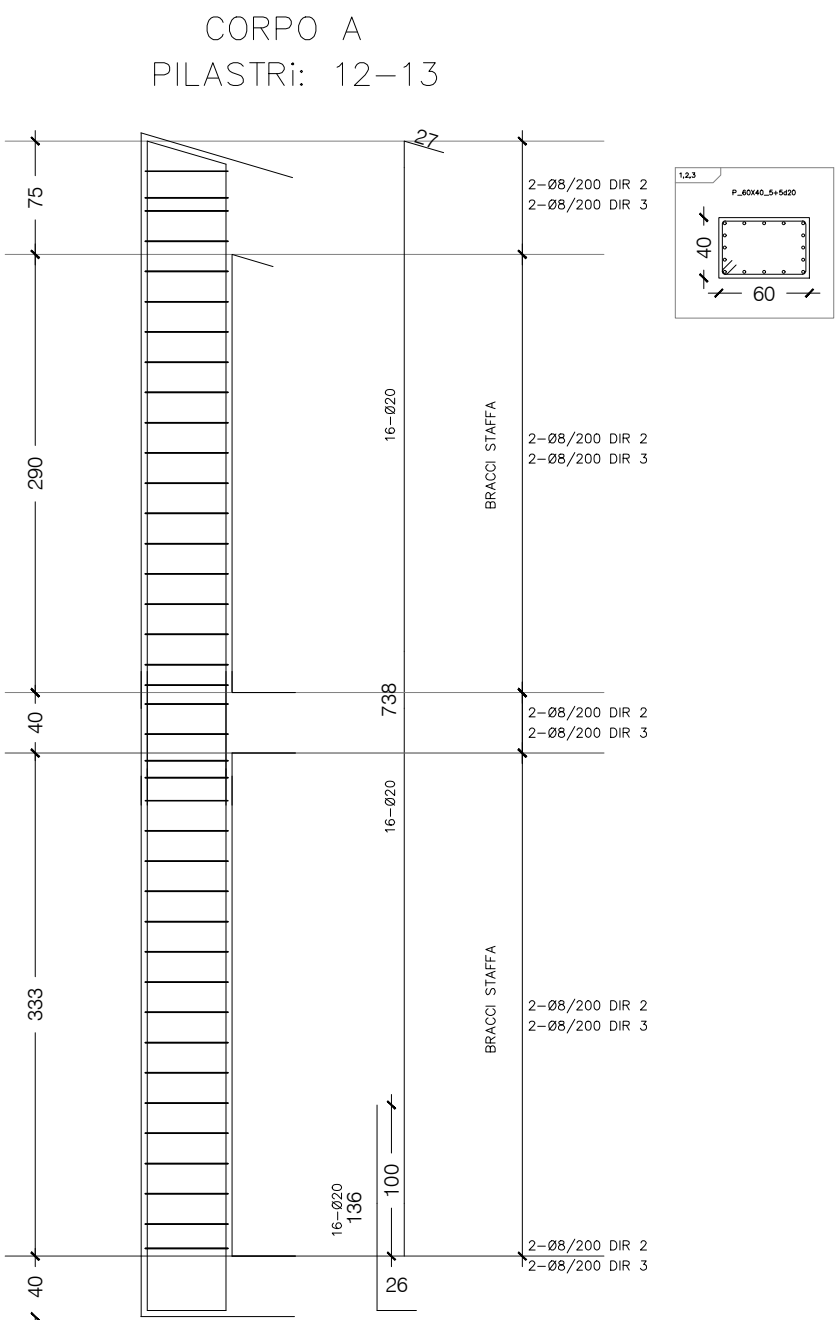
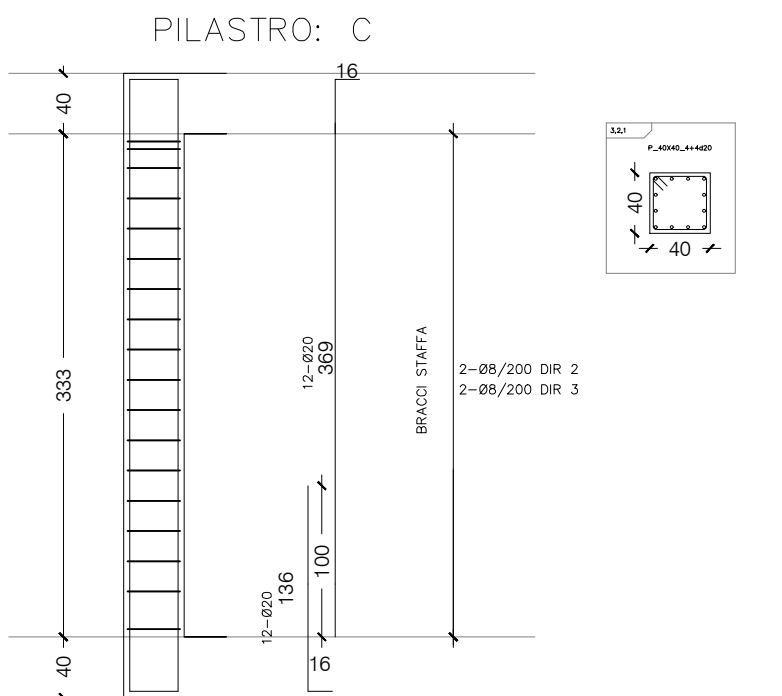
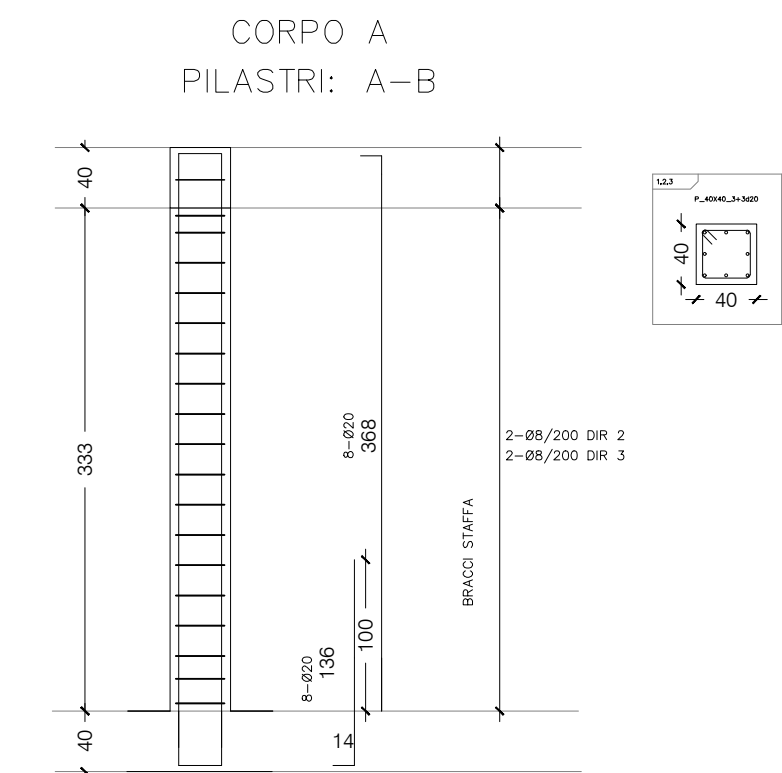
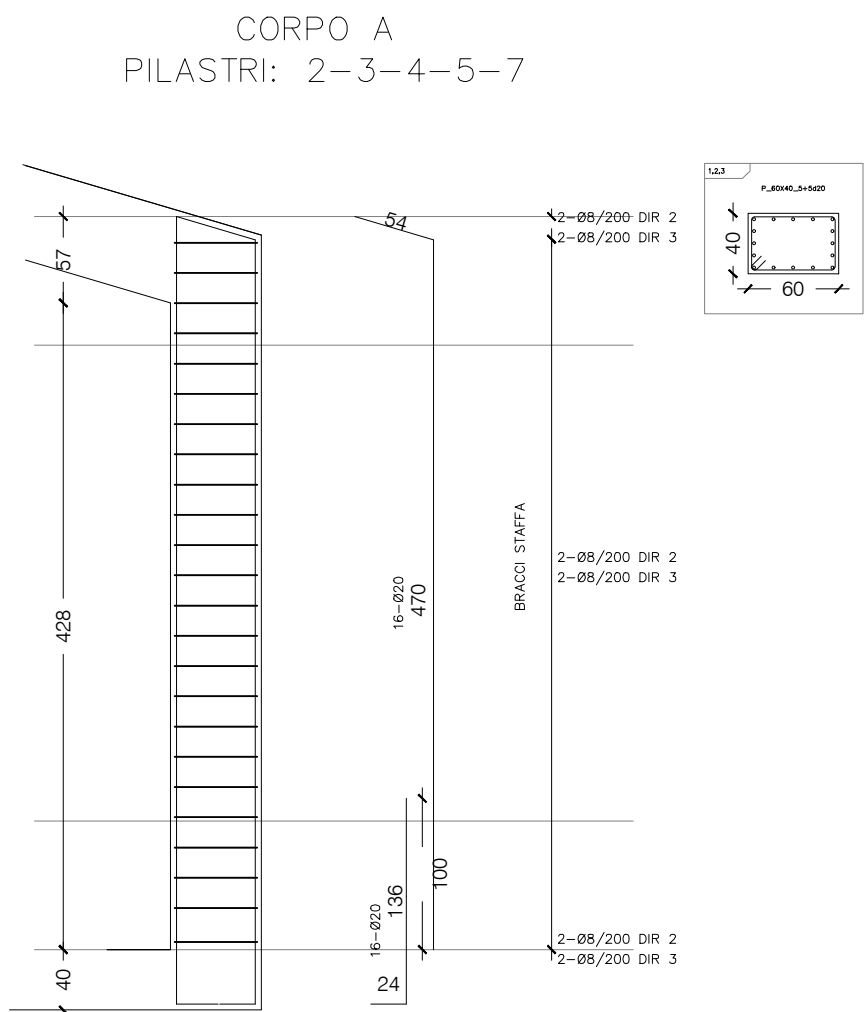
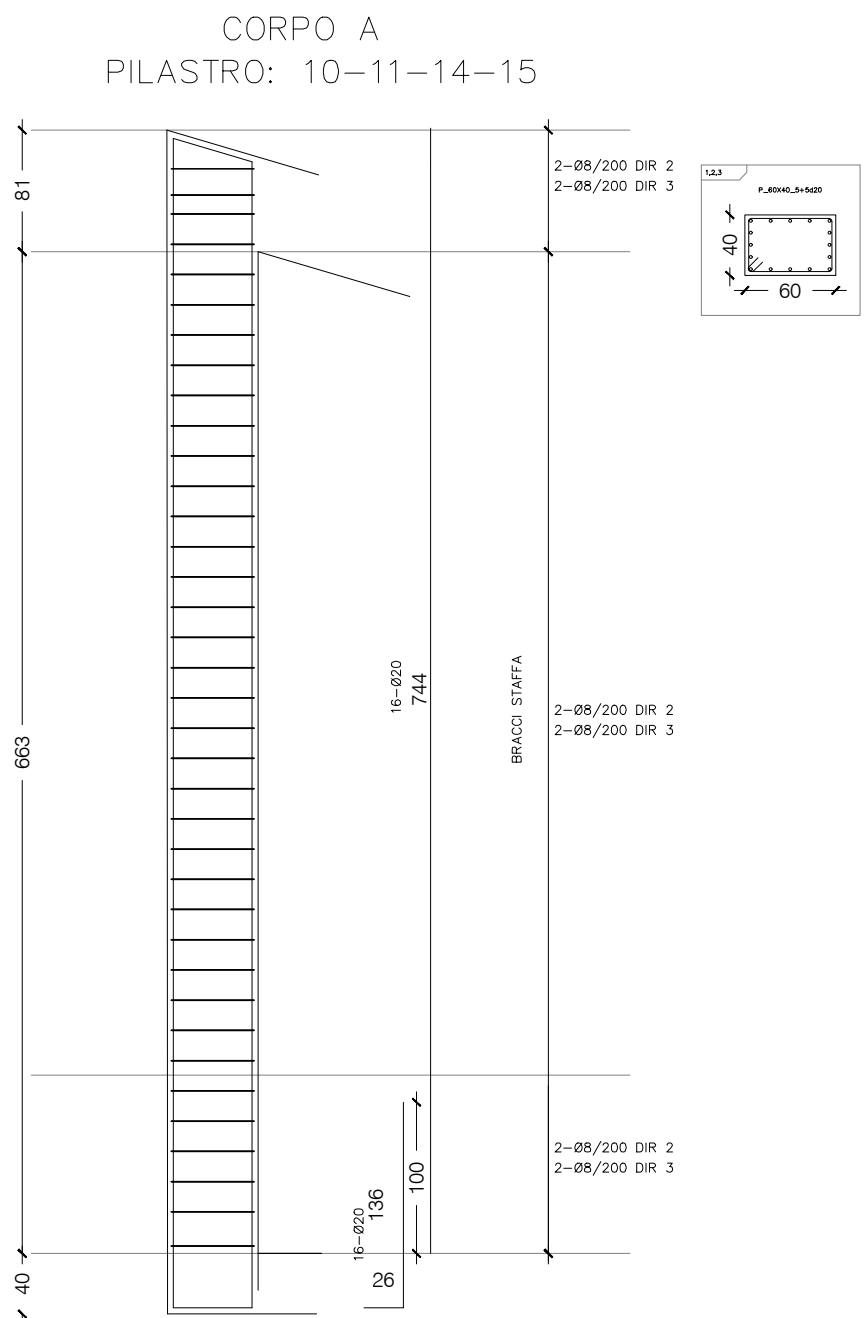


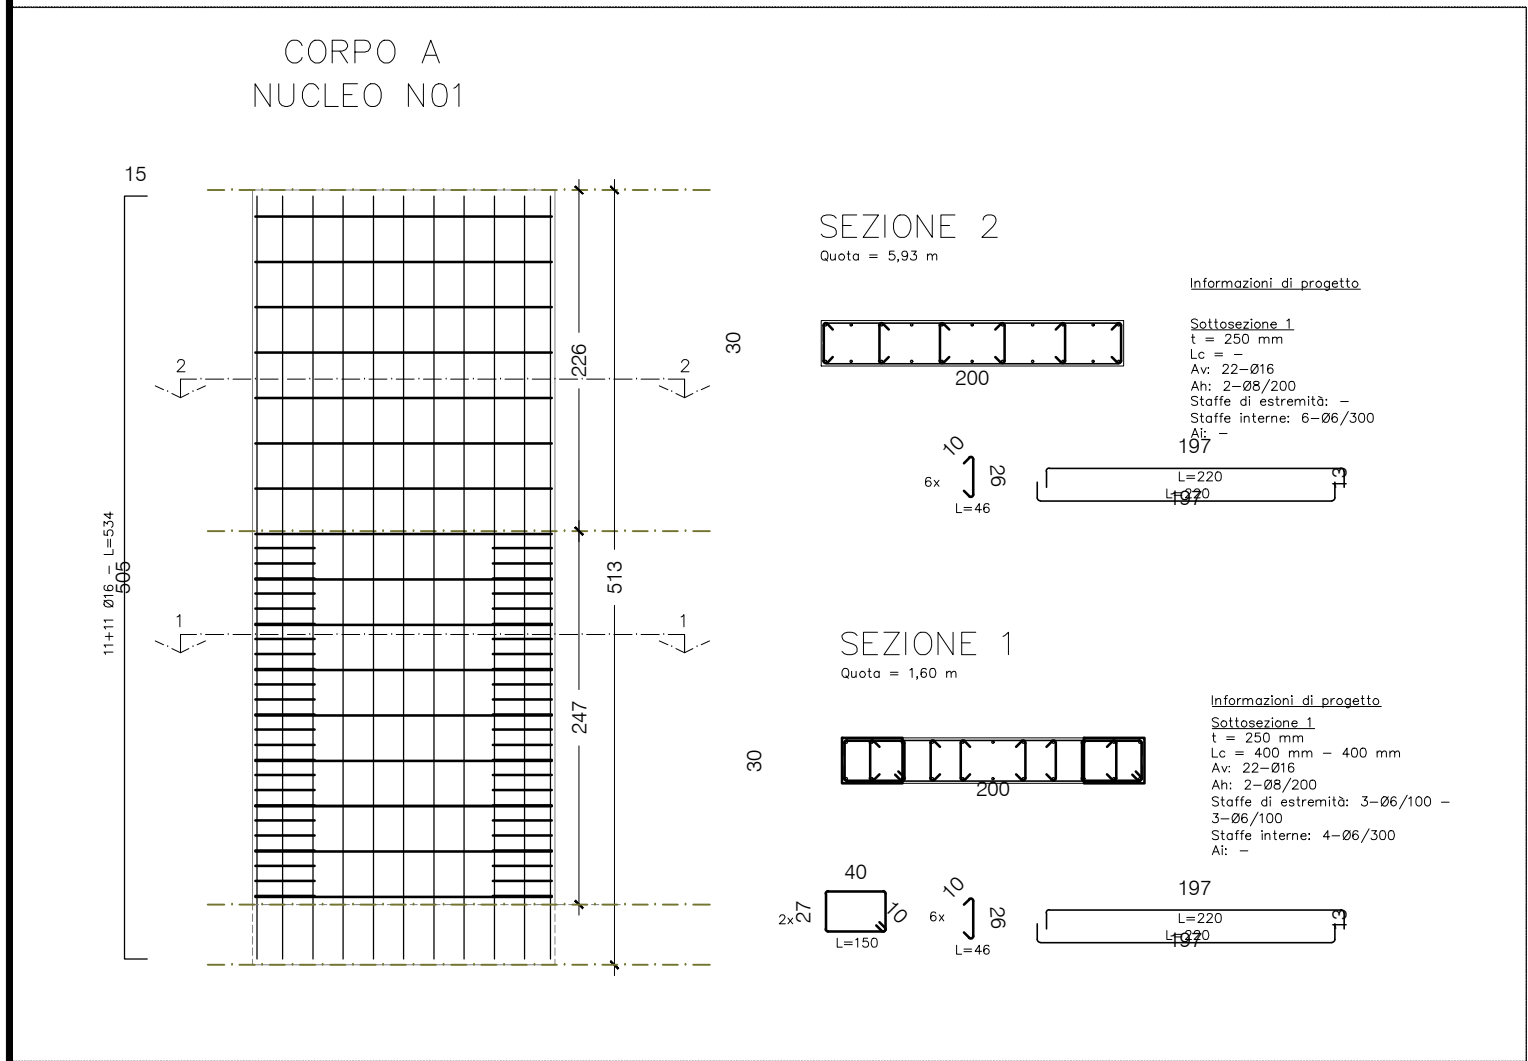

A CAUSA DELLE CONDIZIONI DI COLLABENZA DEL FABBRICATO, E' STATO RISCONTRATO IL RILIEVO DELLO STATO DI FATTO SOLO PARZIALEMENTE E NELLE ZONE DOVE LE CONDIZIONI DI SICUREZZA FOSSERO ASSICURATE. LA RICOSTRUZIONE DELLA CONSISTENZA GEOMETRICA E MATERICA DEI VARI CORPI DI FABBRICA E' STATA ASSUNTA CON RILIEVO DESUNTO DAL PROGETTO DEFINITIVO E TRAMITE VOLO CON DRONE E RICOSTRUZIONE FOTOGRAMMETRICA, PERTANTO ALCUNI AMBIENTI NON SONO RISULTATI ACCESSIBILI. SULLA SCORTA DI QUESTA PREMESSA, UNA VOLTA MESSO IN SICUREZZA IL FABBRICATO DA COLLASSI VARI, VALUTERA' IL DL DI CONCERTO CON LA DITTA ESECUTRICE EVENTUALI DISCOSTAMENTI RISPETTO AL PROGETTO ESECUTIVO CONSEGNATO

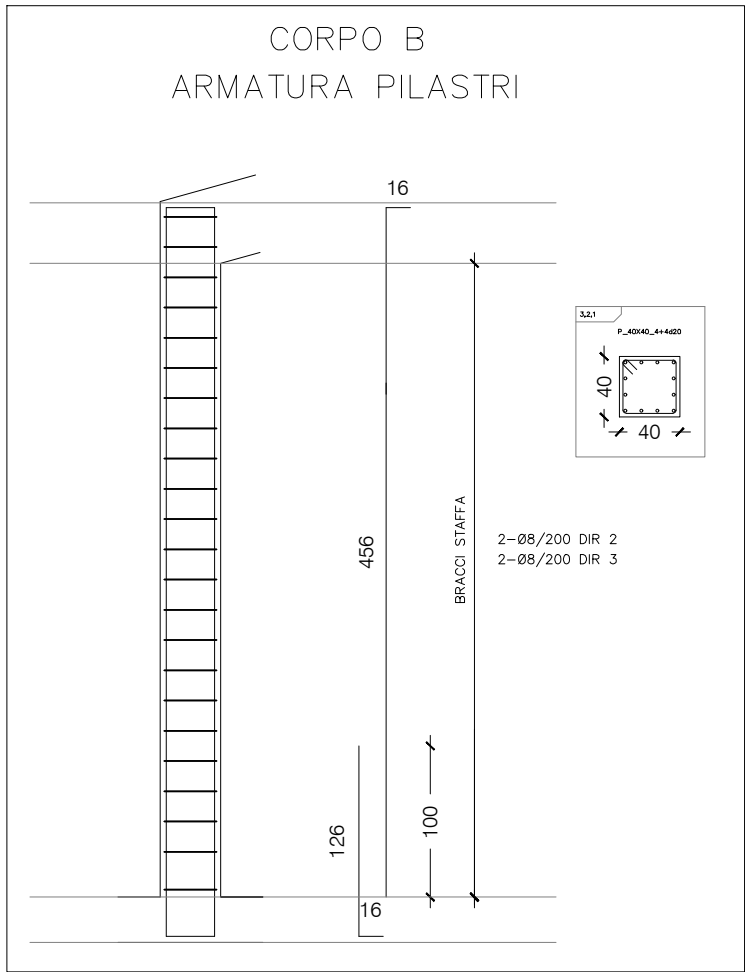

NOTE

TUTTE LE MISURE IN PIANTA SONO IN CM

TUTTE LE QUOTE IN ELEVAZIONE SONO IN M

QUOTA DI RIFERIMENTO RELATIVA +0.00: quota finito piano terra

QUOTA DI RIFERIMENTO RELATIVA +0.00 CORRISPONDE ALLA QUOTA ASSOLUTA +77.5 m slm

FOROMETRIE NEI SETTI

FOROMETRIE NEI SOLAI

NB: le dimensioni ed il posizionamento delle forometrie devono essere verificate e controllate sui progetti architettonico e degli impianti

IN CORRISPONDENZA DEL GIUNTO SISMICO, PREVEDERE A PAVIMENTO, a piano primo e copertura, GIUNTO IMPERMEABILE

MATERIALI

CALCESTRUZZO per magrone	C12/15
CALCESTRUZZO per strutture di fondazione	C25/30
CALCESTRUZZO per strutture in elevazione	C28/35
ACCIAIO PER C.A.	B450C
CLASSE DI ESPOSIZIONE CLS fondazione:	XC2
CLASSE DI ESPOSIZIONE CLS elevazione:	XC1
max a/c (rapporto acqua cemento) 0,60	
Dmax inerti 22 mm per strutture in elevazione	
Dmax inerti 28 mm per strutture di fondazione	
ACCIAIO DA CARPENTERIA:	S273JR
BULLONI:	Classe 8.8

INTERVENTO FINANZIATO DALL'UNIONE EUROPEA - NEXT GENERATION EU CON FONDI PNRR: MSC2: INFRASTRUTTURE SOCIALI, FAMIGLIE, COMUNITA' E TERZO SETTORE - INVESTIMENTO 2.1 PROGETTI DI RIGENERAZIONE URBANA, VOLTI A RIDURRE SITUAZIONI DI EMARGINAZIONE E DEGRADO SOCIALE.

RIQUALIFICAZIONE E VALORIZZAZIONE AMBIENTALE E TURISTICA DEL PARCO DI MONTELUNGO E AREE ANNESSE - C.DA MONTELUNGO

Stazione Appaltante:

COMUNE DI GELA
LIBERO CONSORZIO COMUNALE DI CALTANISSETTA

Sede legale Piazza San Francesco, 1 93012 Gela (CL)
tel. 0933 906680 - pec: comune.gela@pec.comune.gela.cl.it
P.IVA e C.F.: 01409860853

Responsabile Unico del Procedimento:
Ing. Stefano Sammartino
e-mail: s.sammartino@comune.gela.cl.it

Impresa:

EMMA LAVORI COOP. S.C.A.R.L.
Sede legale San Cataldo (CL) - Piazza degli Eroi n. 2, 93017
tel. 0934 594188 - e-mail: info@emmalavori.it
P.I. e C.F.: 01409860853

RTP Progettisti:

MANDATARIA:
Studio AARC.it
Livorno (LI), Via G.M. Terreni, 32 - 57122
tel 0586169086 fax 0586014808 - e-mail: aarc@aacr.it
P.I. e C.F.: 01858520495 D. Menichetti arch. - V.Menichini Arch.

MANDANTE:
Geol. Giuseppe Lamia
Trapani (TP) - Via Tripoli, 19 - 91100
tel. 3291472241 - e-mail: lamiagiuseppe@gmail.com
P.I.: 02329420810 - C.F. LMAGPP80D22D423R


Collaboratore progetto struttura:
Ing. Francesco Pellegrini
Collaboratore progetto impianti:
Ing. Francesco Sambo

Fase del progetto: **Progetto esecutivo**

Disciplina: **Elaborato generale**

Elaborato: **Corpo A e Corpo B - Dettagli di armatura: elevazione**

Codice elaborato: **PE.2S.GN.GE.ARM.015.00**

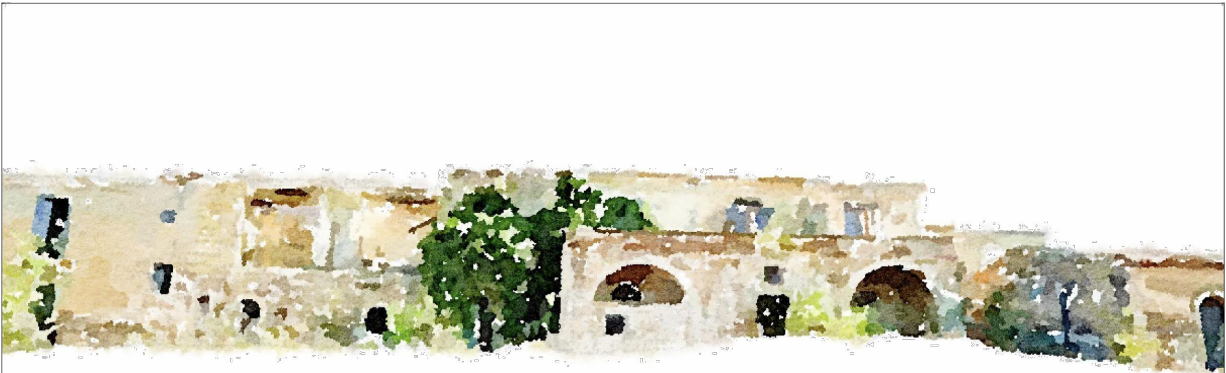

REV. N° 0	DATA REV.	Data: 09/08/2024
		Scala: