


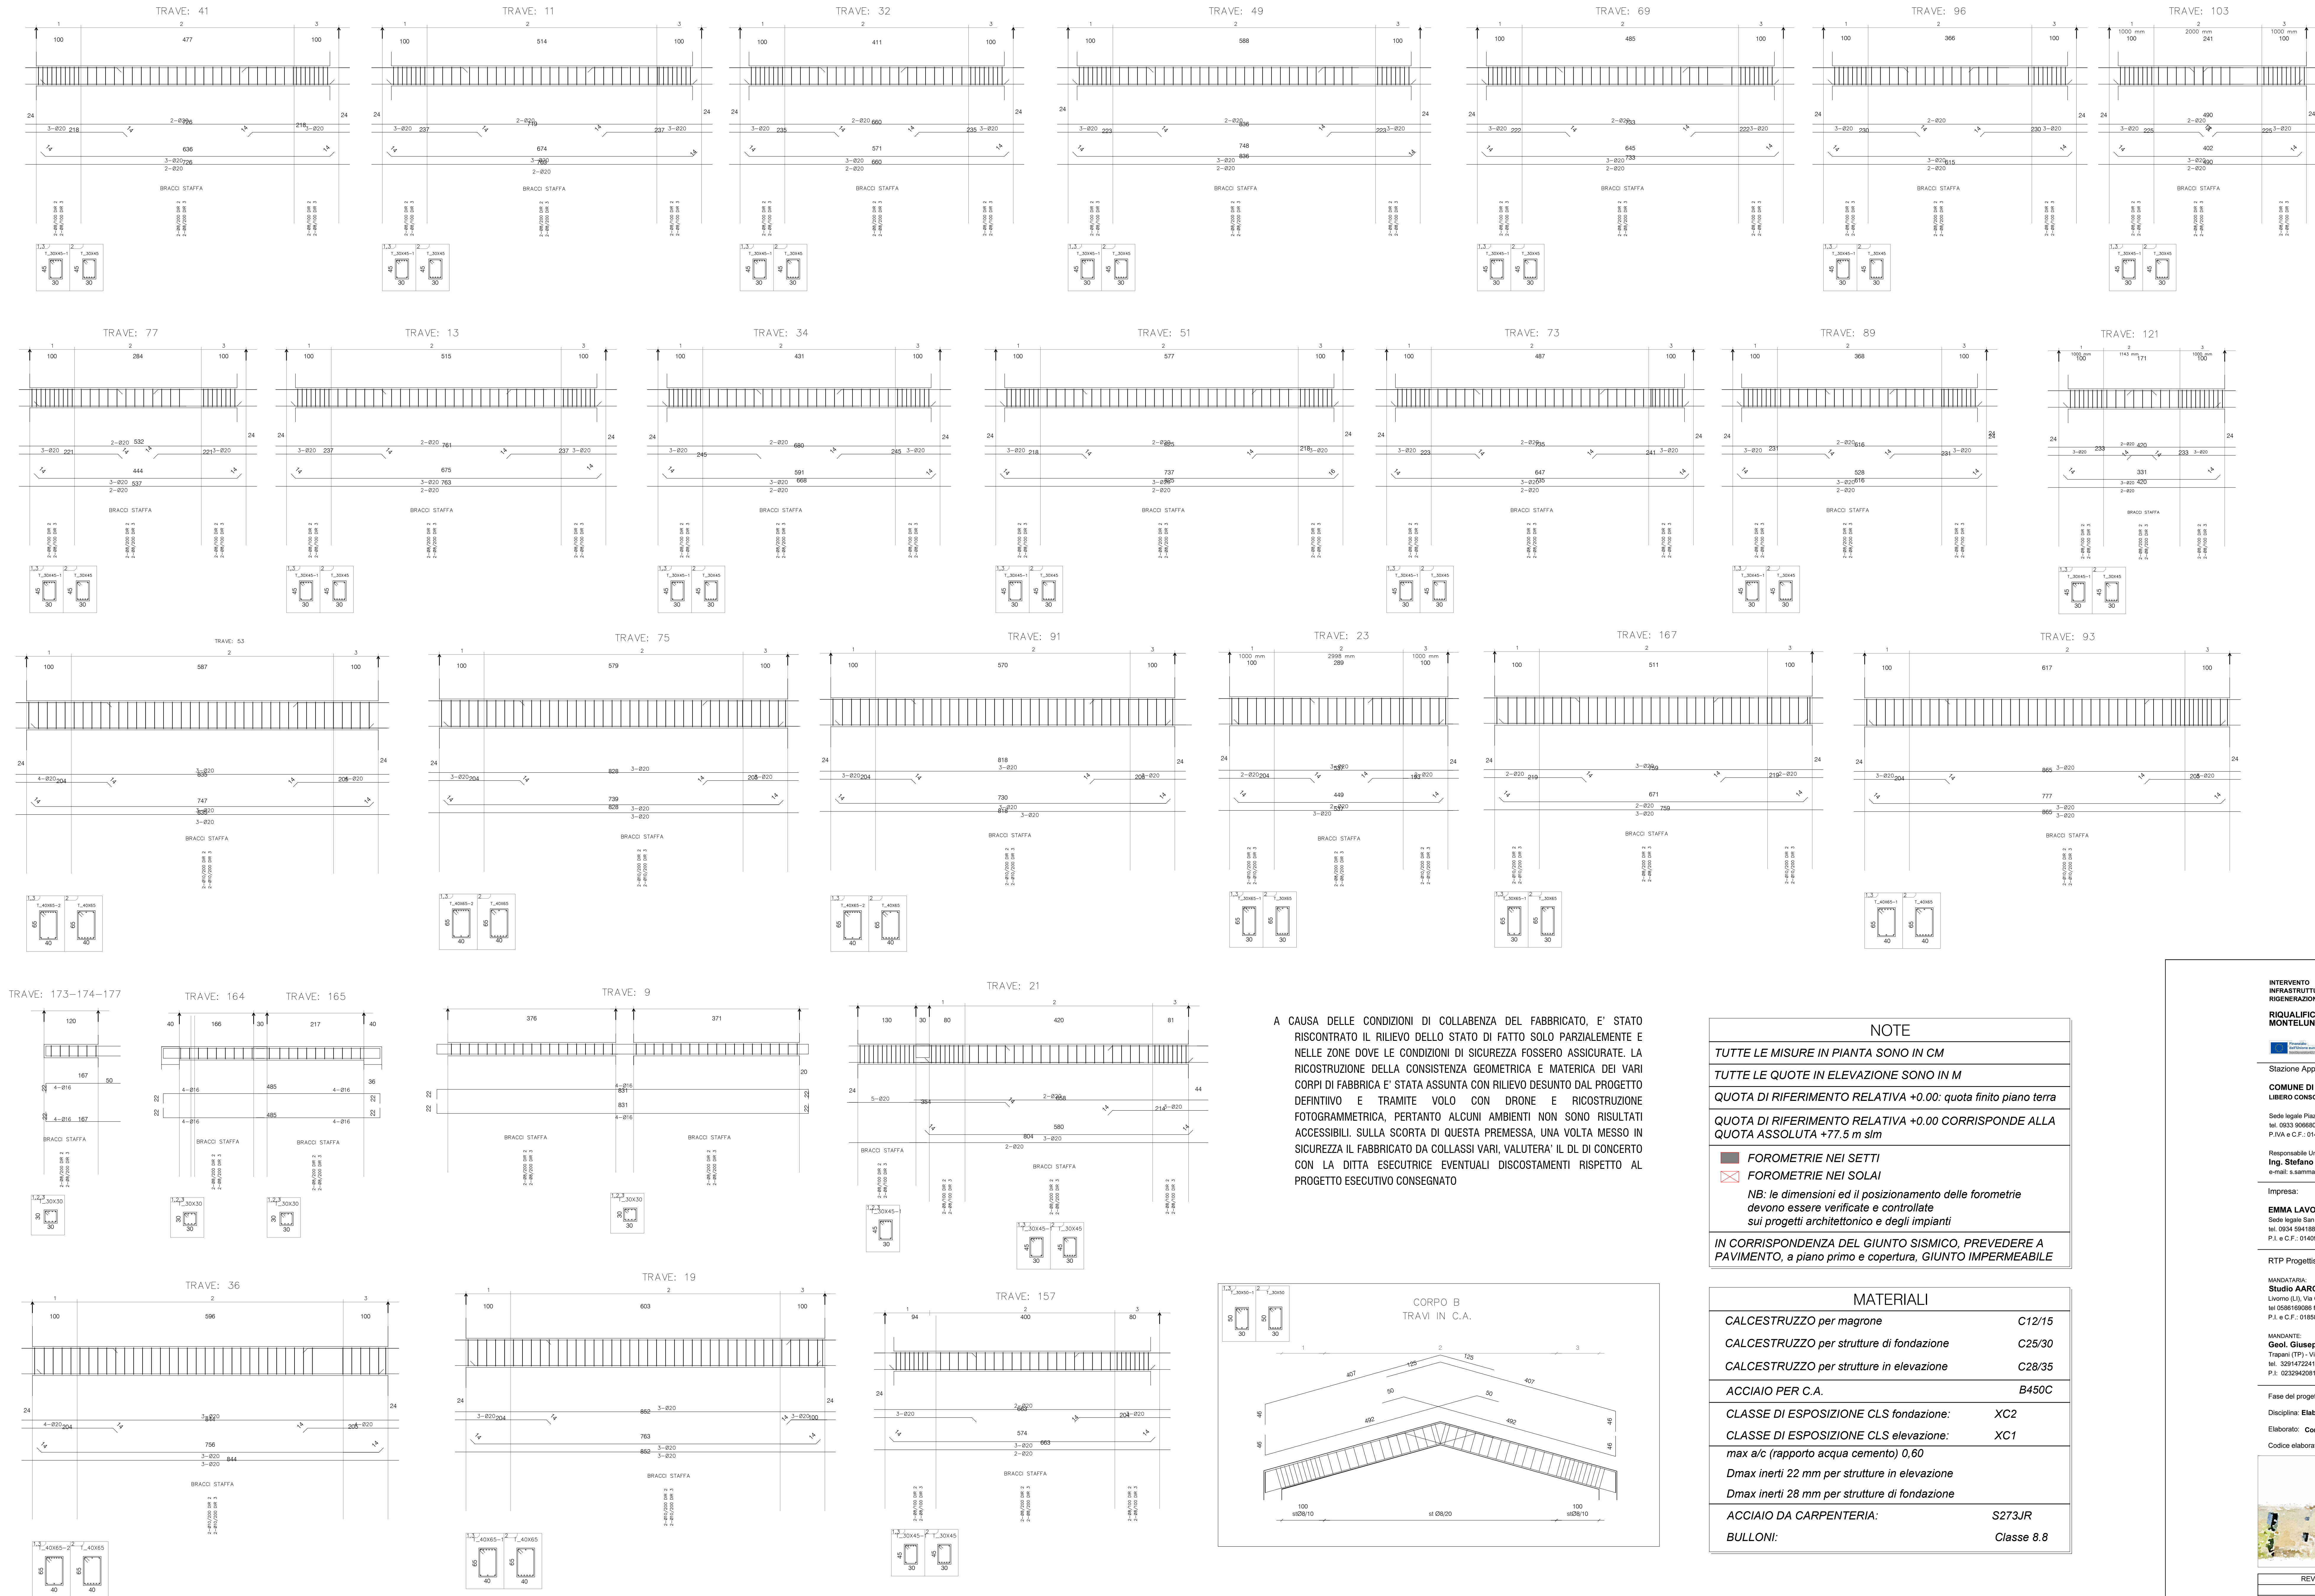

A CAUSA DELLE CONDIZIONI DI COLLABENZA DEL FABBRICATO, E' STATO RISCOVRATO IL RILIEVO DELLO STATO DI FATTO SOLO PARZIALEMENTE E NELLE ZONE DOVE LE CONDIZIONI DI SICUREZZA FOSSERO ASSICURATE. LA RICOSTRUZIONE DELLA CONSISTENZA GEOMETRICA E MATERICA DEI VARI CORPI DI FABBRICA E' STATA ASSUNTA CON RILIEVO DESUNTO DAL PROGETTO DEFINITIVO E TRAMITE VOLO CON DRONE E RICOSTRUZIONE FOTOGRAMMETRICA, PERTANTO ALCUNI AMBIENTI NON SONO RISULTATI ACCESSIBILI. SULLA SCORTA DI QUESTA PREMESSA, UNA VOLTA MESSO IN SICUREZZA IL FABBRICATO DA COLLASSI VARI, VALUTERA' IL DL DI CONCERTO CON LA DITTA ESECUTRICE EVENTUALI DISCOSTAMENTI RISPETTO AL PROGETTO ESECUTIVO CONSEGNATO

NOTE	
TUTTE LE MISURE IN PIANTA SONO IN CM	
TUTTE LE QUOTE IN ELEVAZIONE SONO IN M	
QUOTA DI RIFERIMENTO RELATIVA +0.00: quota finito piano terra	
QUOTA DI RIFERIMENTO RELATIVA +0.00 CORRISPONDE ALLA QUOTA ASSOLUTA +77.5 m slm	
FOROMETRIE NEI SETTI FOROMETRIE NEI SOLAI NB: le dimensioni ed il posizionamento delle forometrie devono essere verificate e controllate sui progetti architettonico e degli impianti	
IN CORRISPONDENZA DEL GIUNTO SISMICO, PREVEDERE A PAVIMENTO, a piano primo e copertura, GIUNTO IMPERMEABILE	

MATERIALI	
CALCESTRUZZO per magrone	C12/15
CALCESTRUZZO per strutture di fondazione	C25/30
CALCESTRUZZO per strutture in elevazione	C28/35
ACCIAIO PER C.A.	B450C
CLASSE DI ESPOSIZIONE CLS fondazione:	XC2
CLASSE DI ESPOSIZIONE CLS elevazione:	XC1
max a/c (rapporto acqua cemento) 0,60	
Dmax inerti 22 mm per strutture in elevazione	
Dmax inerti 28 mm per strutture di fondazione	
ACCIAIO DA CARPENTERIA:	S273JR
BULLONI:	Classe 8.8

INTERVENTO FINANZIATO DALL'UNIONE EUROPEA - NEXT GENERATION EU CON FONDI PNRR: MSC2: INFRASTRUTTURE SOCIALI, FAMIGLIE, COMUNITA' E TERZO SETTORE - INVESTIMENTO 2.1 PROGETTI DI RIQUALIFICAZIONE URBANA, VOLTA A RIGIURARE SITUAZIONI DI EMARGINAZIONE E DEGRADO SOCIALE.

Stazione Appaltante: **CLP** 033D21002180001 **CIG** A0120CD443

COMUNE DI GELA

Sede legale Piazza San Francesco, 1 93012 Gela (CL)
tel. 0253 908581 - pec: comune.gela@pec.comune.gela.it
P.IVA e C.F.: 01408680853

Responsabile Unico del Procedimento:
Ing. Stefano Sammartino
e-mail: s.sammartino@comune.gela.it

Impresa:

EMMA LAVORI COOP. S.C.A.R.L.
Sede legale San Cataldo (CL) - Piazza degli Eroi n. 2, 93017
tel. 0324 594198 - e-mail: info@emmalavori.it
P.I. e C.F.: 01409680853

RTP Progettisti:

MANDATARIA:
Studio AACR.it
Livorno (LI) - Via G.M. Terreni, 33 - 57122
tel. 0586169066 fax 0586014508 - e-mail: aacr@aacr.it
P.I. e C.F.: 01858520495 D. Menichetti arch. - V. Menichetti Arch.

MANDANTE:
Geol. Giuseppe Lami
Trapani (TP) - Via Trapani, 10 - 91100
tel. 3291472241 - e-mail: lamigiuseppe@gmail.com
P.I. 02328420810 - C.F. LMAGPP80D220423R

Fase del progetto: **Progetto esecutivo**

Disciplina: **Elaborato generale**

Elaborato: **Corpo A e Corpo B - Dettagli di armatura: travi**

Codice elaborato: **PE.25.GN.GE.ARM.016.00**



REV. N° 0	DATA REV.	Data: 09/09/2024
		Scala: